


JAPAZ  
GUERRA  
ARQUITECTOS

OBRA:

**ARIZU**

GODOY CRUZ / MENDOZA

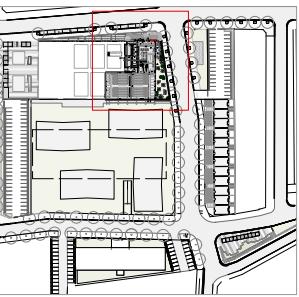

# SECTOR G

Auditorio

Godoy cruz / Mendoza / Argentina

PLANO:


Portada

FECHA


ESCALA -

PLANO N° G.0


REV.

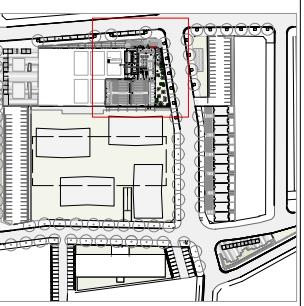

PLANO:  
Planta  
FECHA  
ESCALA 1:200  
PLANO N° G.1 REV.

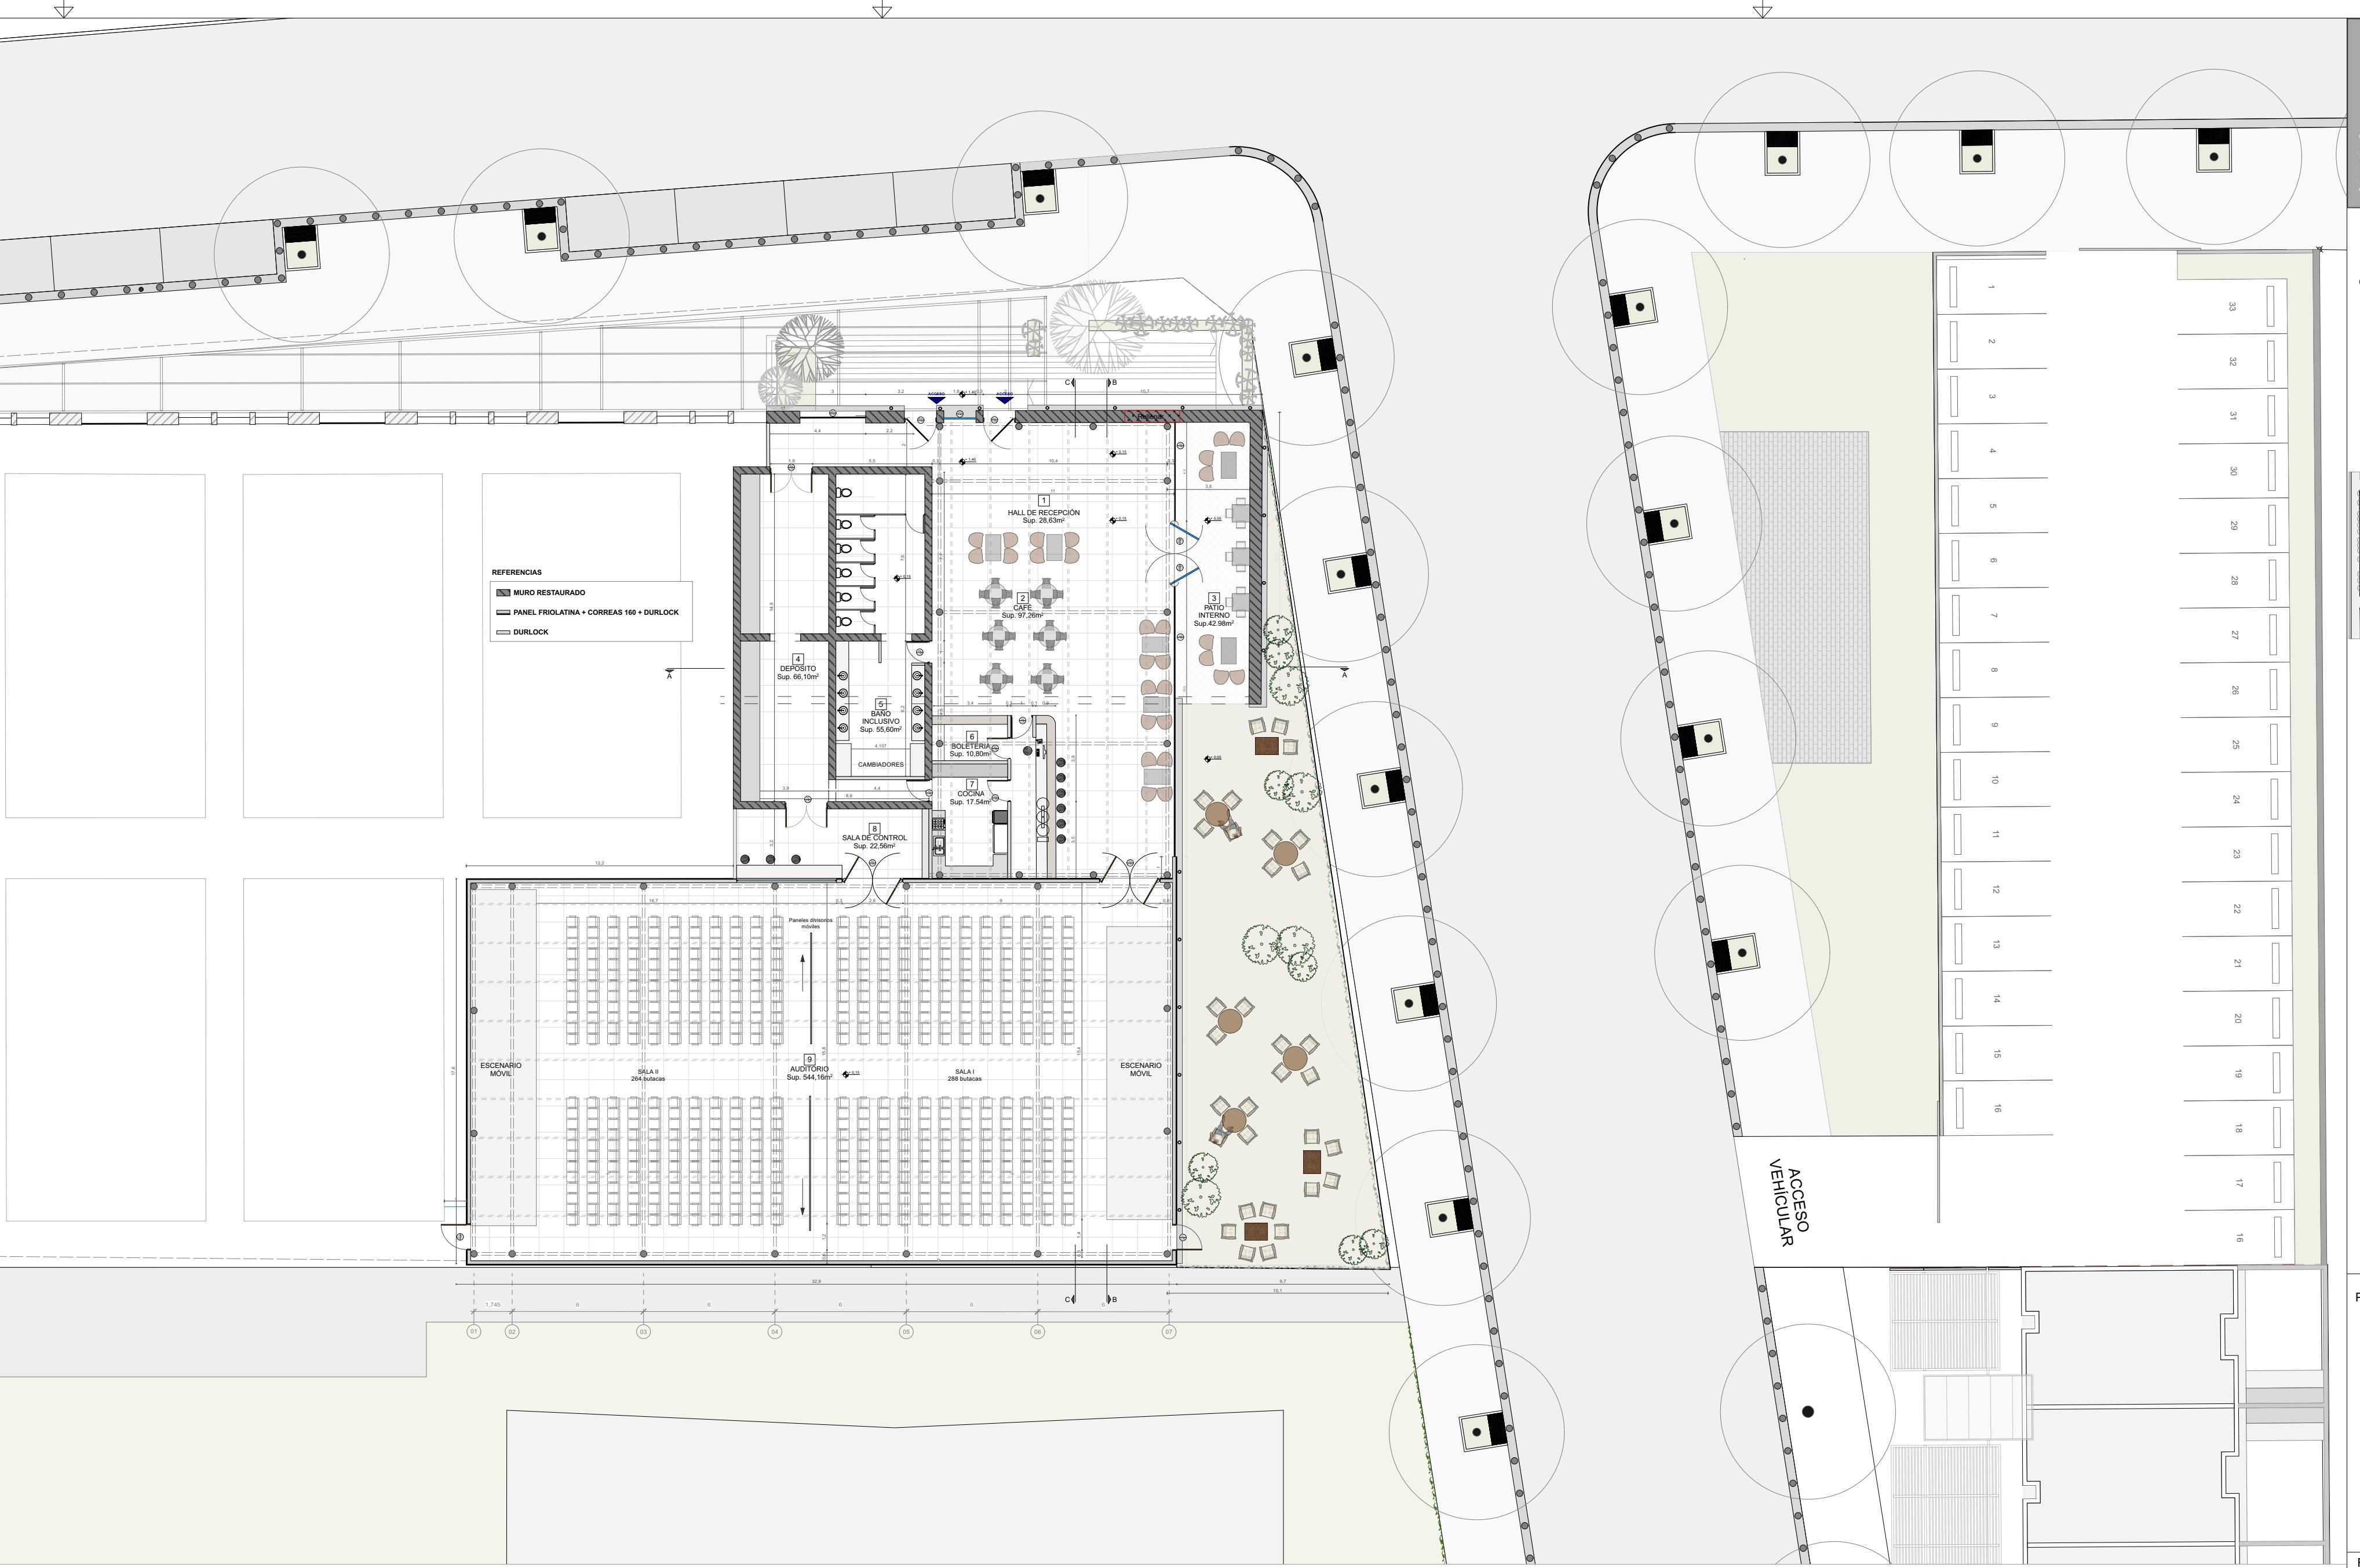





1 Planta auditorio  
Scale: 1:200

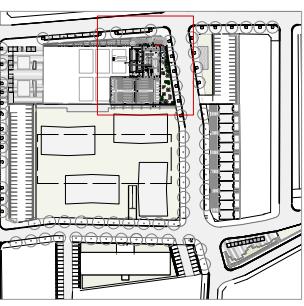


PLANO:  
Planta de techos

FECHA  
ESCALA 1:200  
PLANO N° G.2 REV.

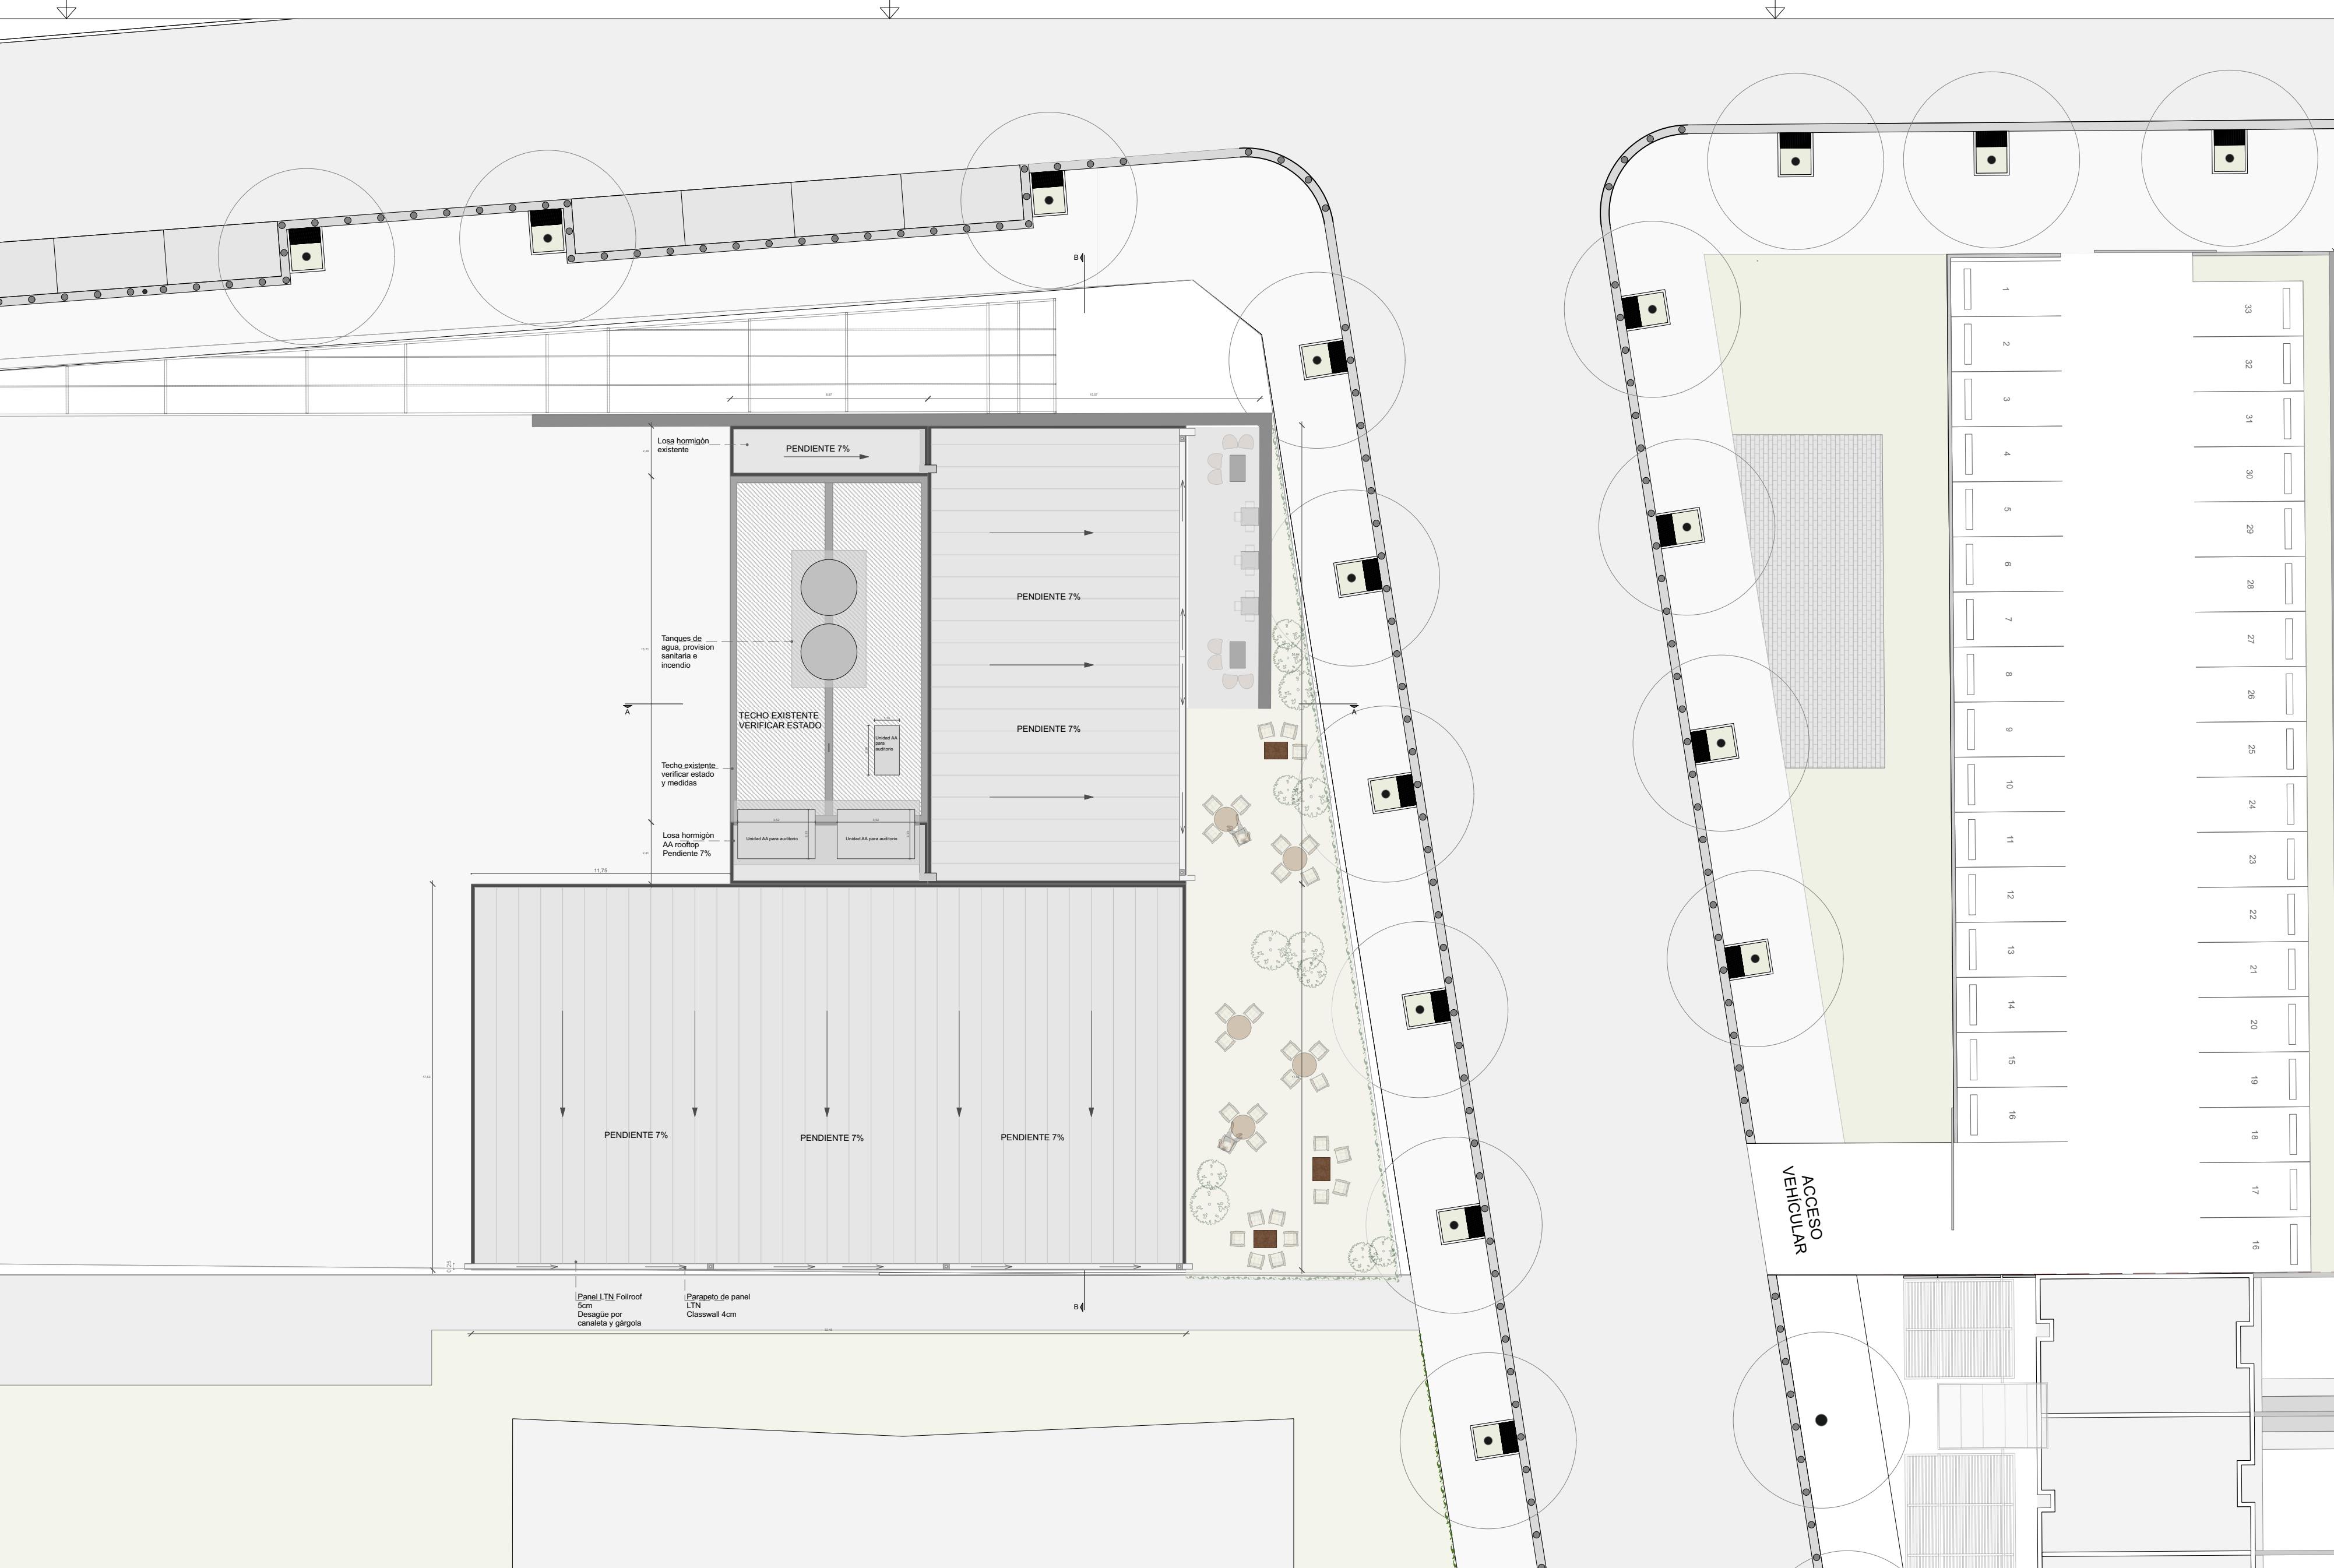

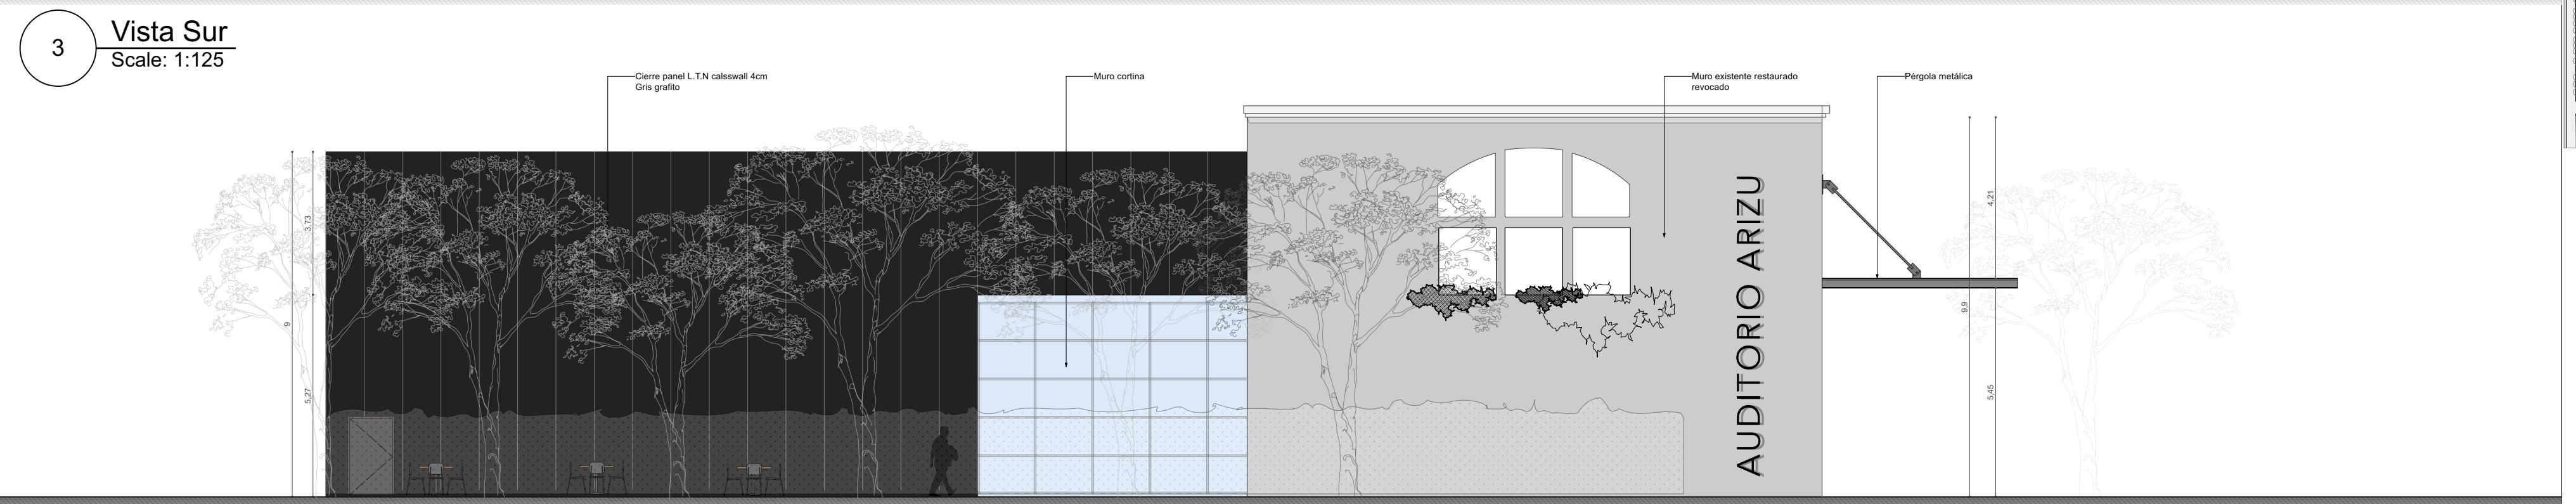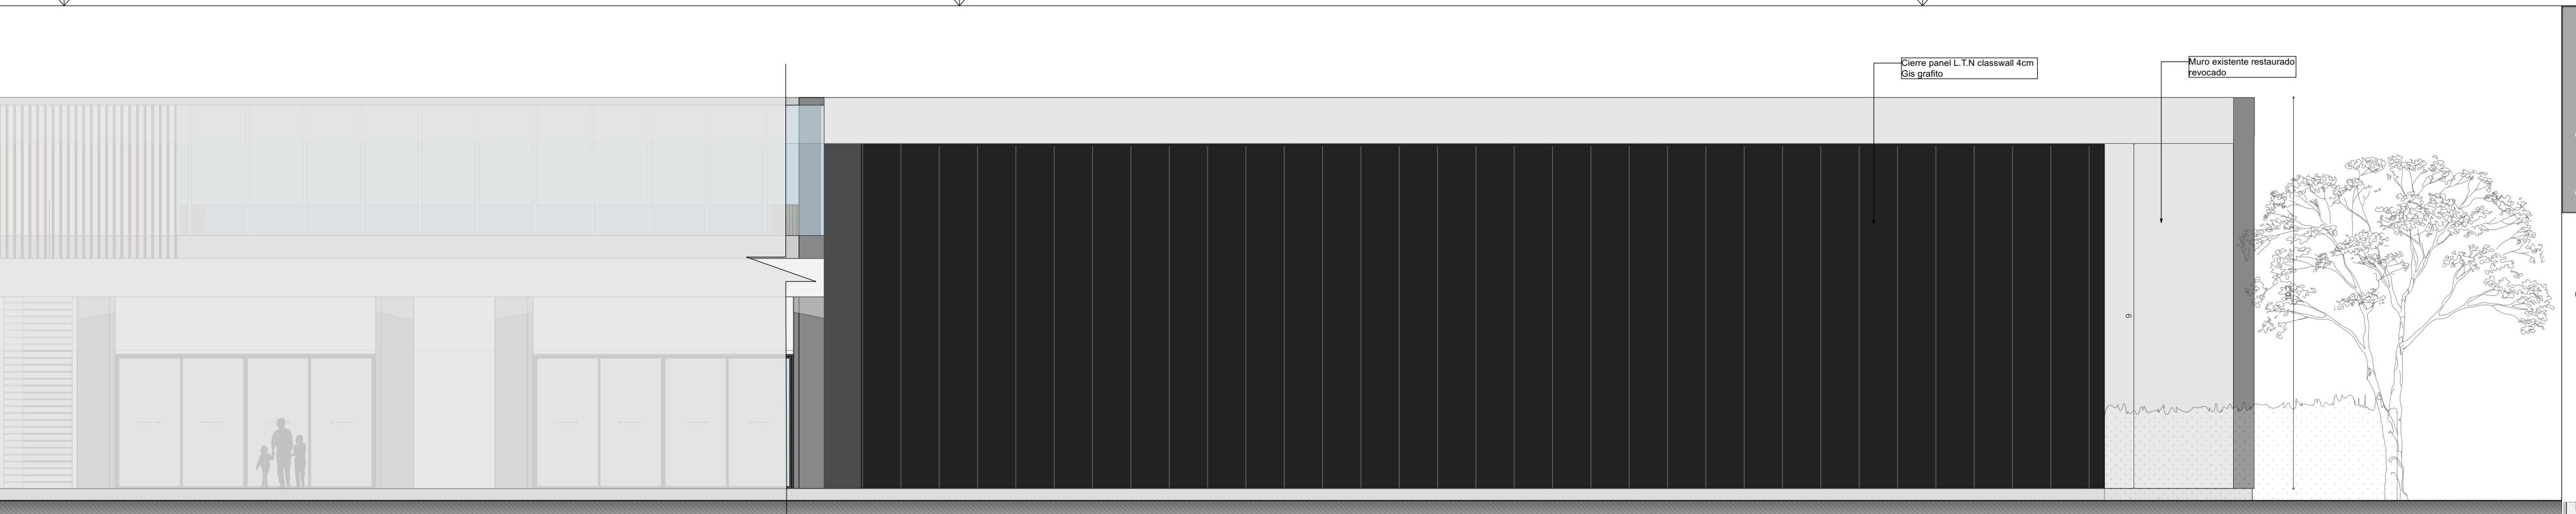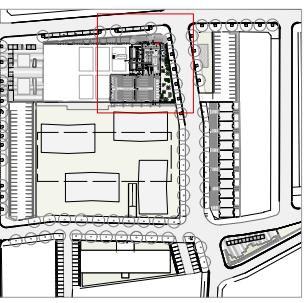

PLANO:  
Vistas  
FECHA \_\_\_\_\_  
ESCALA 1:125  
PLANO N° G.3 REV. \_\_\_\_\_

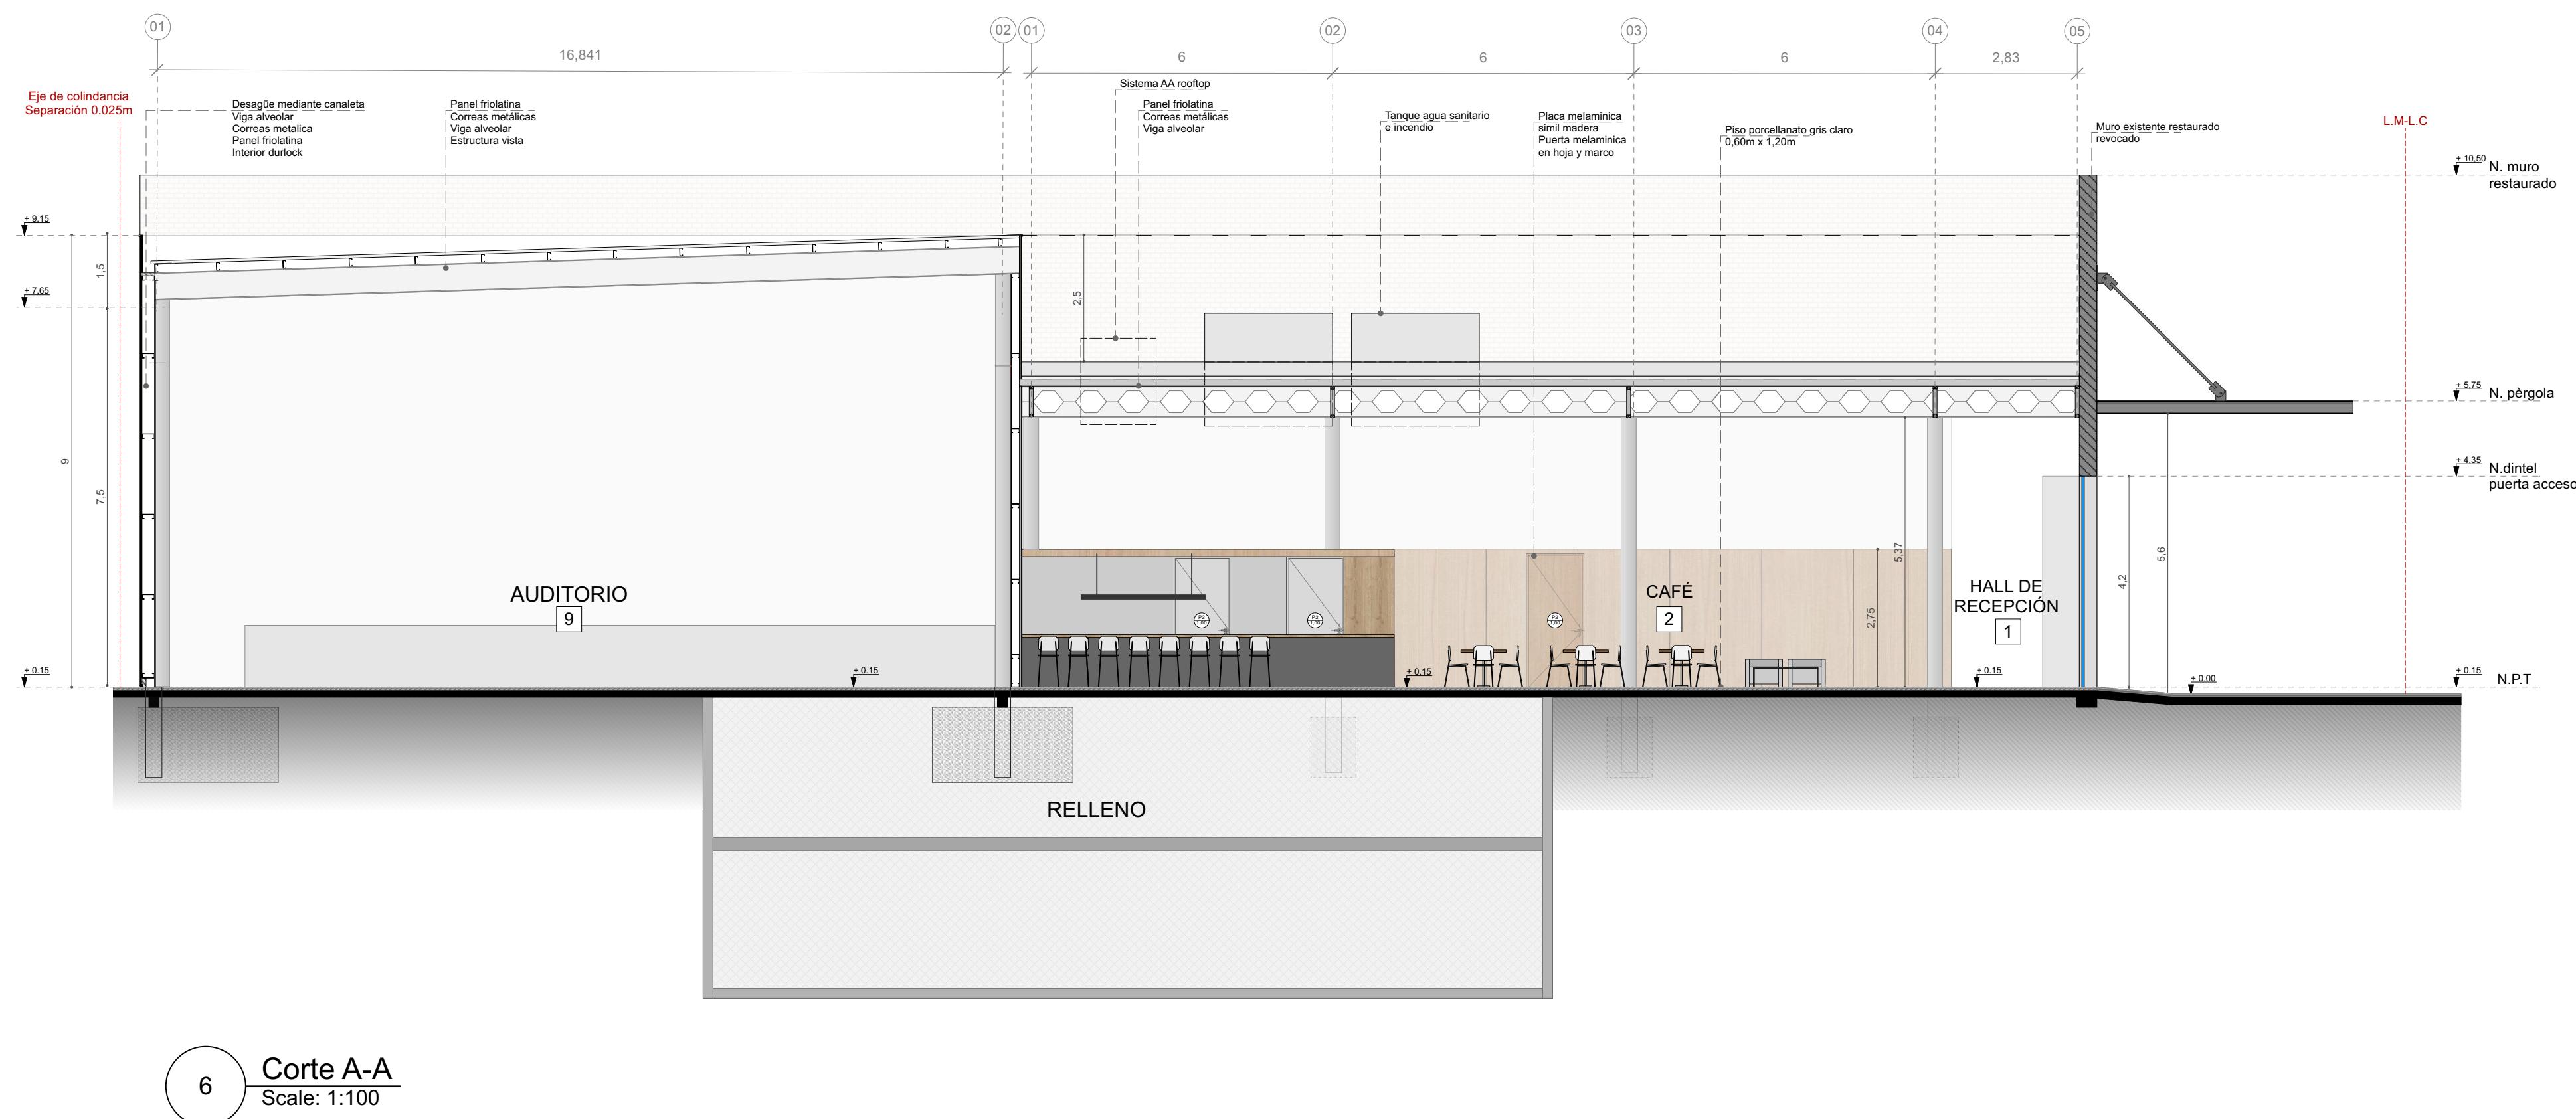

PLANO:


Corte A-A

FECHA

ESCALA 4/100

---

For more information about the study, please contact Dr. [REDACTED] at [REDACTED].

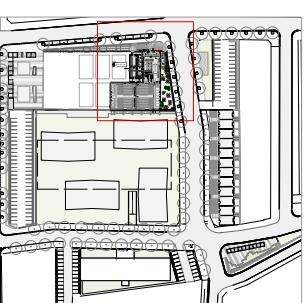



PLANO:  
Corte B-B



FECHA

ESCALA 1:100


PLANO N° G.5

REV.

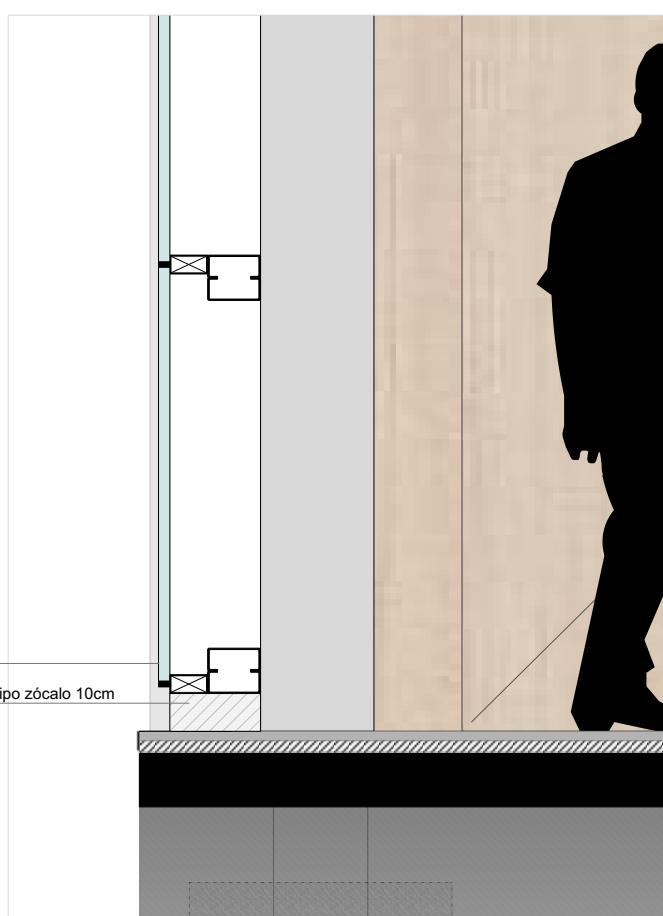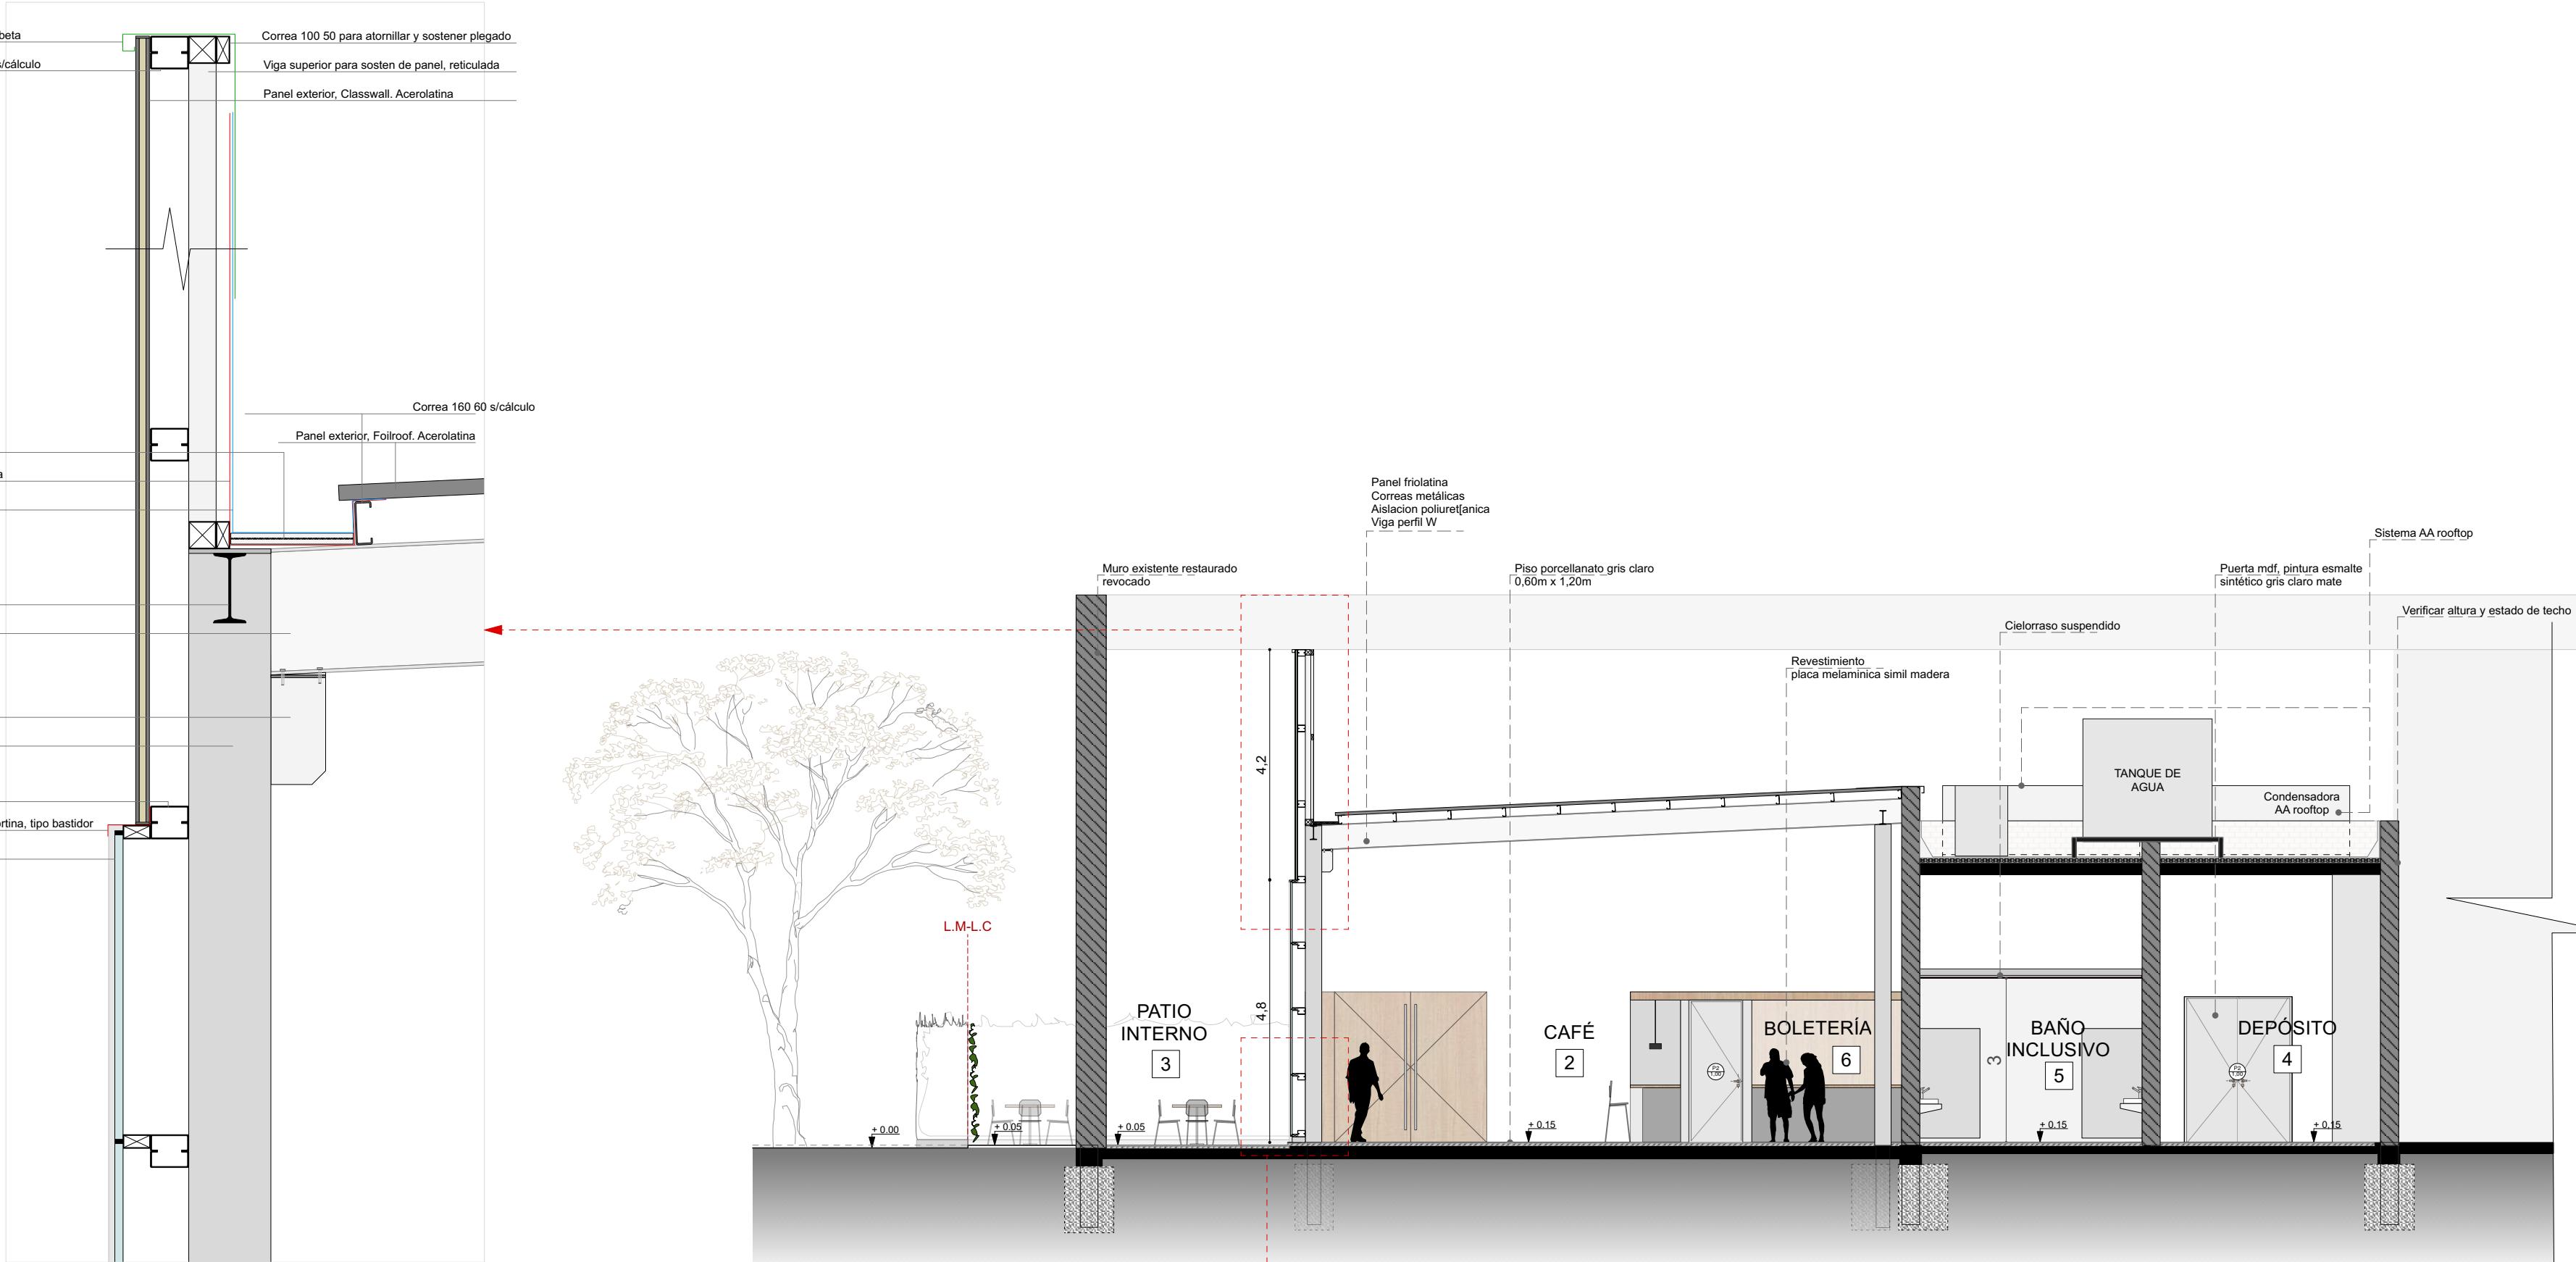

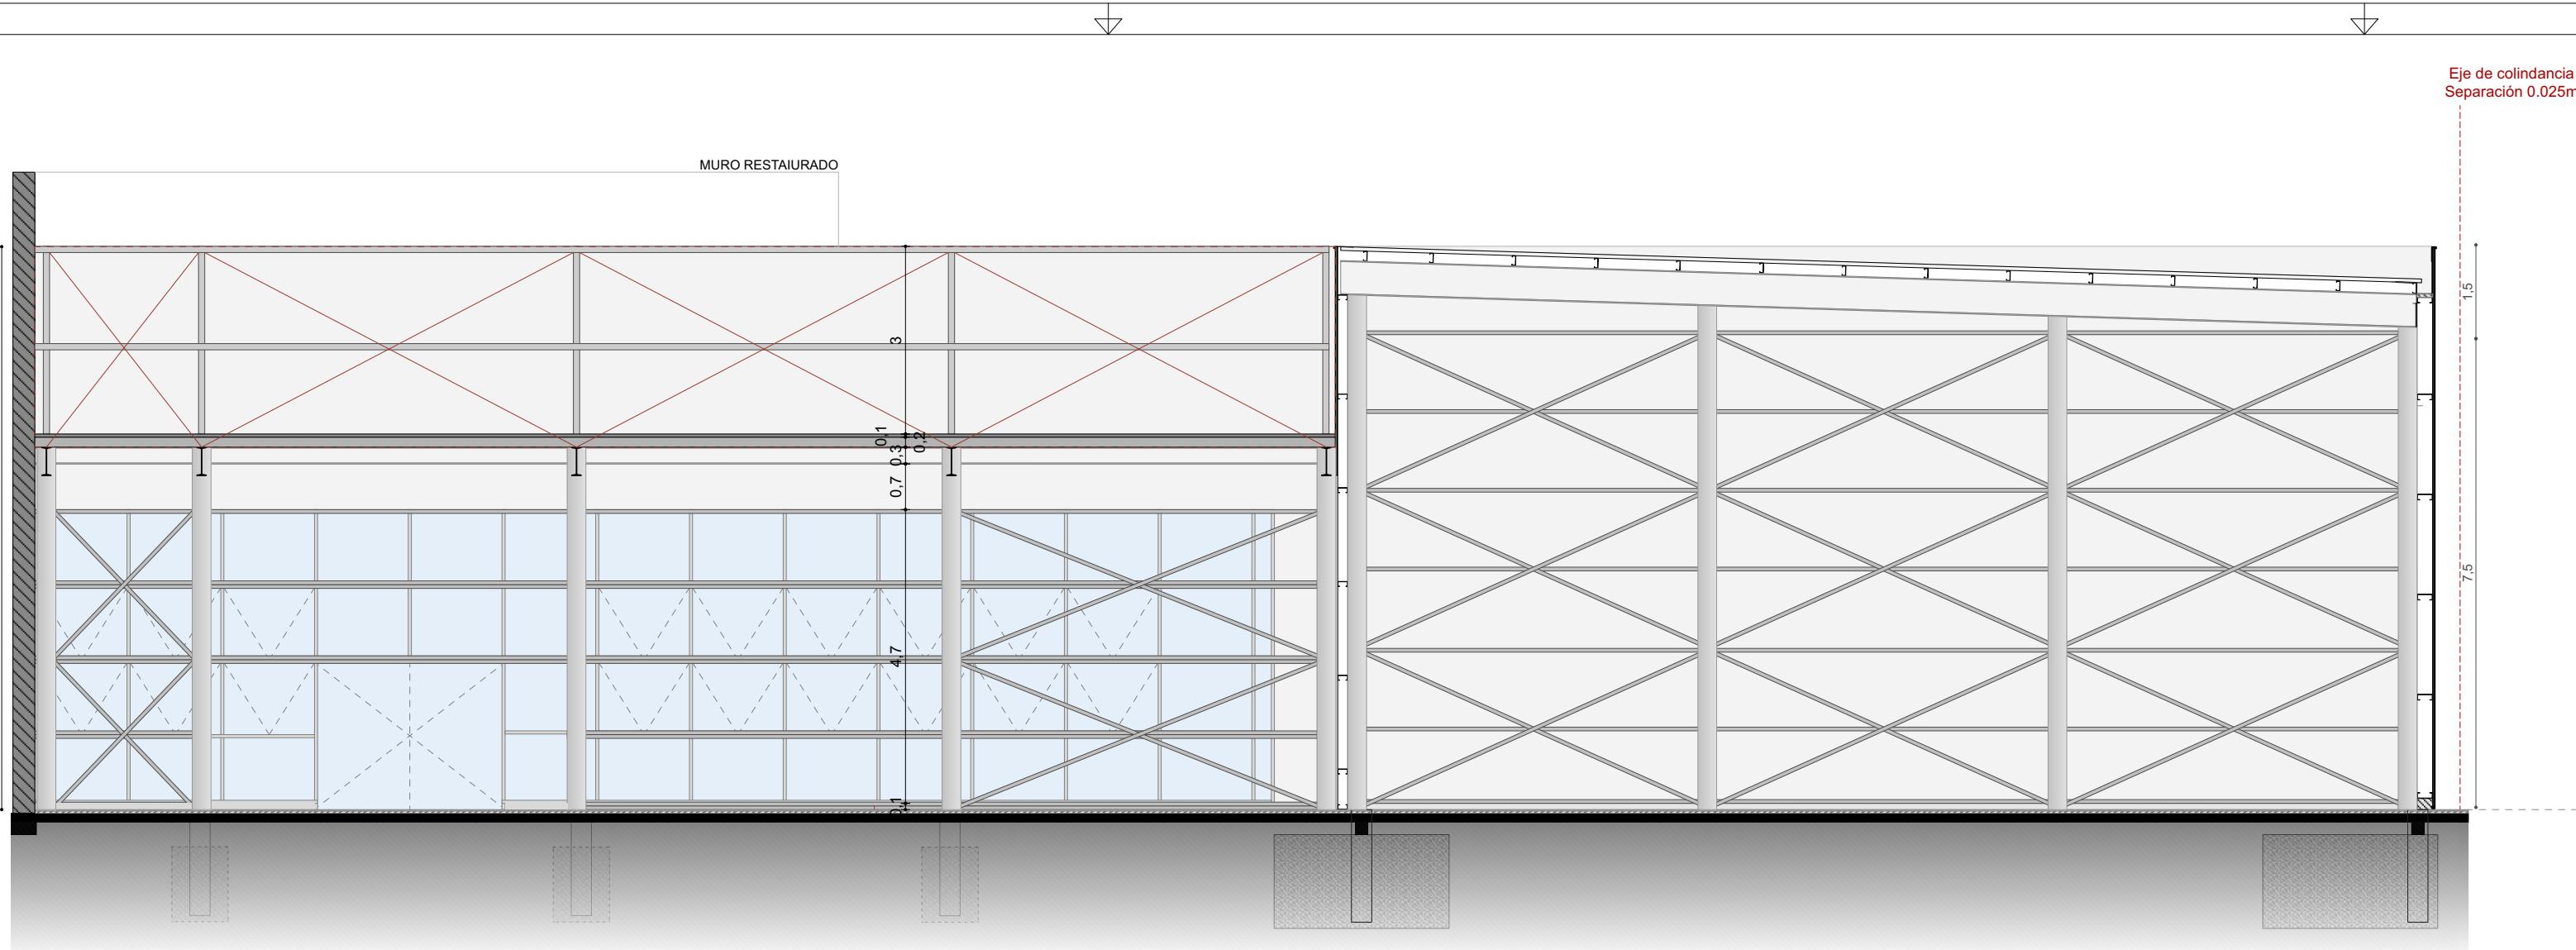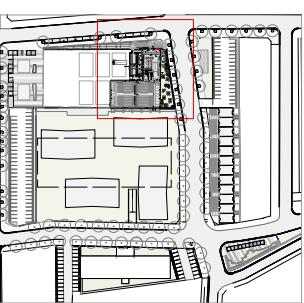


8 Corte C-C  
Scale: 1:100

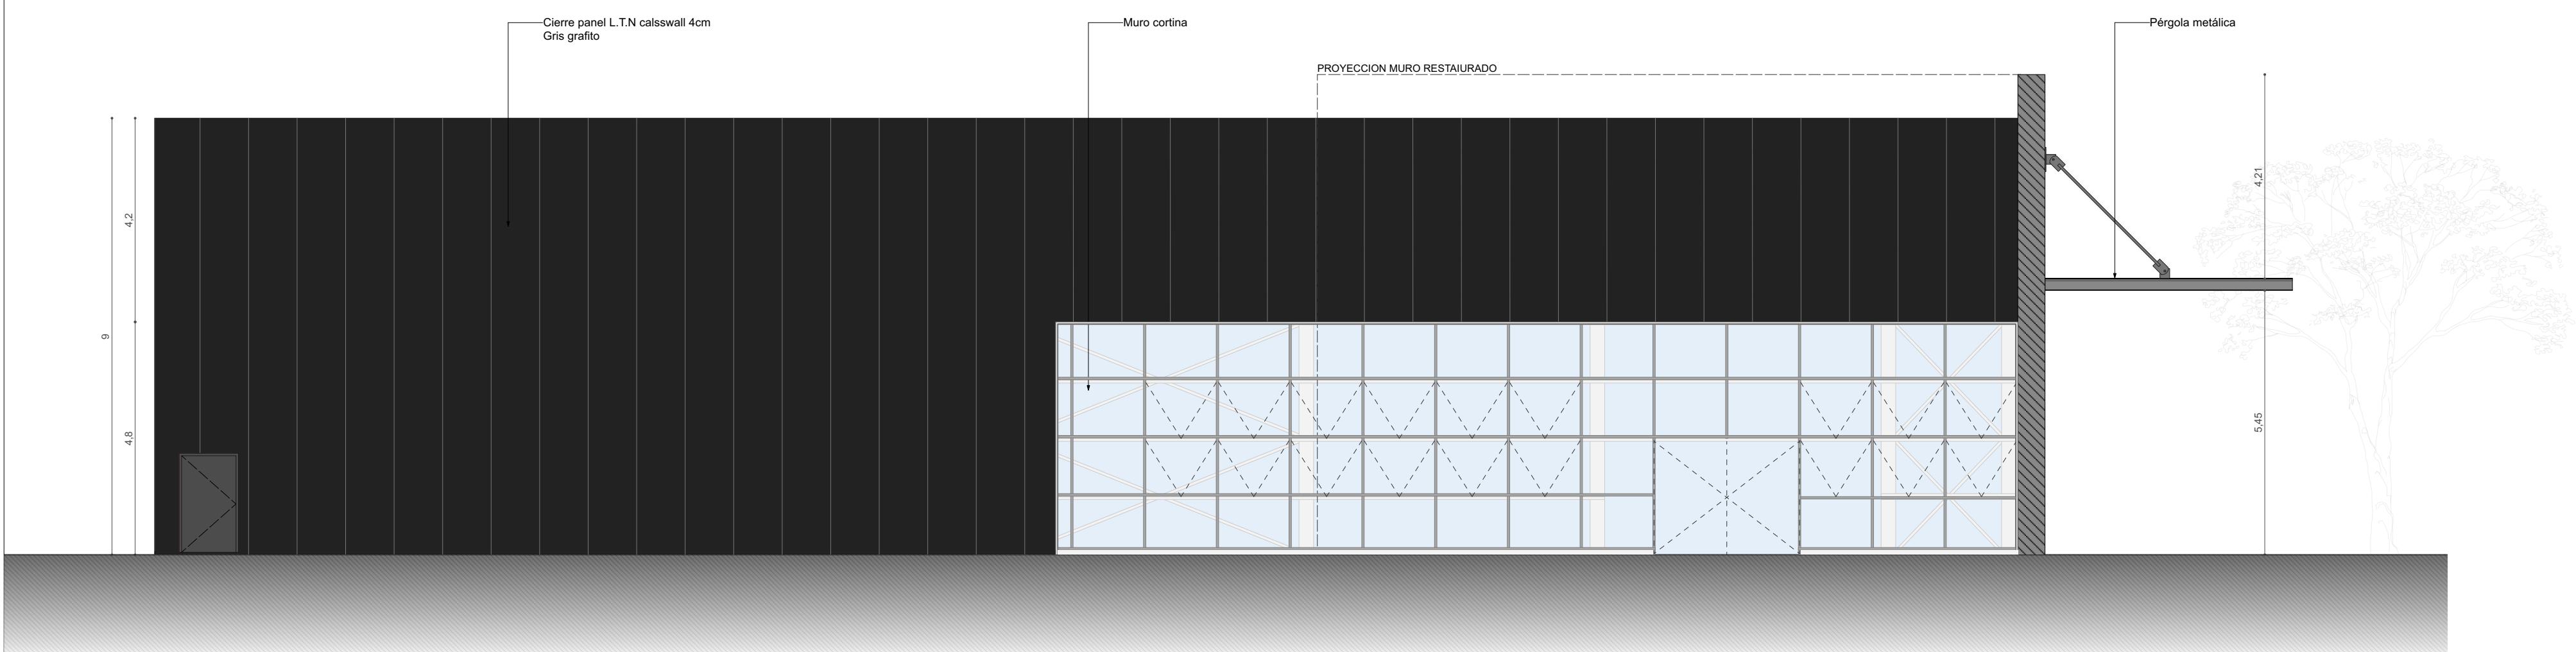

9 Vista fachada este interna a patio interior  
Scale: 1:100

PLANO:  
Corte C-C y vista

FECHA	
ESCALA 1:100	
PLANO N° G.6	REV.

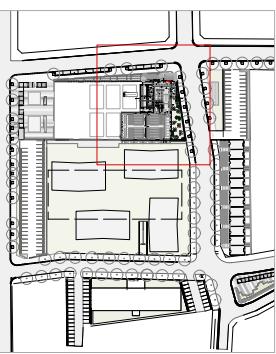


## PANELES - VISTA A-A

M2 TOTALES DE  
PANEL 291,5 m<sup>2</sup>

DESIGNACIÓN	①	①	①	①	①	①
VISTA GENERAL						
VISTA						
TIPO	PANEL 1*9	PANEL 0,395 *9				
CANTIDAD	32 (treinta y dos)	1 (uno)				
COLOR	Gris grafito	Gris grafito				

1 PANELES VISTA A-A  
Scale: 1:100

PLANO:  
Paneles vista Sur  
FECHA  
ESCALA  
PLANO N° G.7 REV.

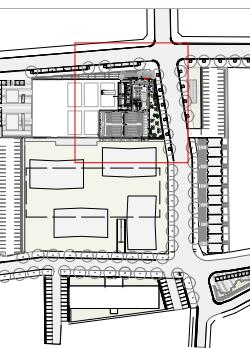

## PANELES - VISTA B-B


M<sup>2</sup> TOTALES DE  
PANEL 232,5 m<sup>2</sup>

DESIGNACIÓN	①	①	①	①	①	①
VISTA GENERAL						
VISTA						
TIPO	PANEL 1*9	PANEL 1*9	PANEL 1*9	PANEL 1*9	PANEL 1,00*0,3804	PANEL 0,532*0,3804
CANTIDAD	1 (uno)	1 (uno)	16 (quince)	16 (quince)	21 (veintiuno)	1 (uno)
COLOR	Gris grafito	Gris grafito				

2 PANELES VISTA B-B  
Scale: 1:100

PLANO:  
Paneles vista Este

FECHA  
ESCALA  
PLANO N° G.8 REV.

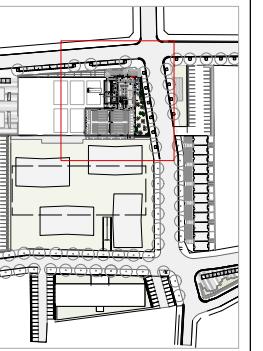

## PLANTA DE TECHOS

M<sup>2</sup> TOTALES DE  
PANEL 549,5m<sup>2</sup>

DESIGNACIÓN	1	1	1	1	1	1
<b>VISTA</b>						
PENDIENTE 7%	PENDIENTE 7%	PENDIENTE 7%				
0,25						
Panel LTN Foilroof 5cm Desagüe por canaleta y gárgola	Parapeto de panel LTN Classwall 4cm					
TIPO	PANEL 1*17,091	PANEL 0.147*17,091				
CANTIDAD	32 (treinta y dos)	1 (uno)				
COLOR	Gris grafito	Gris grafito				

3 PLANTA DE TECHOS SUR  
Scale: 1:100


PLANO:  
Paneles planta de techos  
auditorio

FECHA  
ESCALA  
PLANO N° G.9 REV.


# PLANTA DE TECHOS

M2 TOTALES DE  
PANEL 231,6m<sup>2</sup>

DESIGNACIÓN	1	1	1	1	1	1
-------------	---	---	---	---	---	---

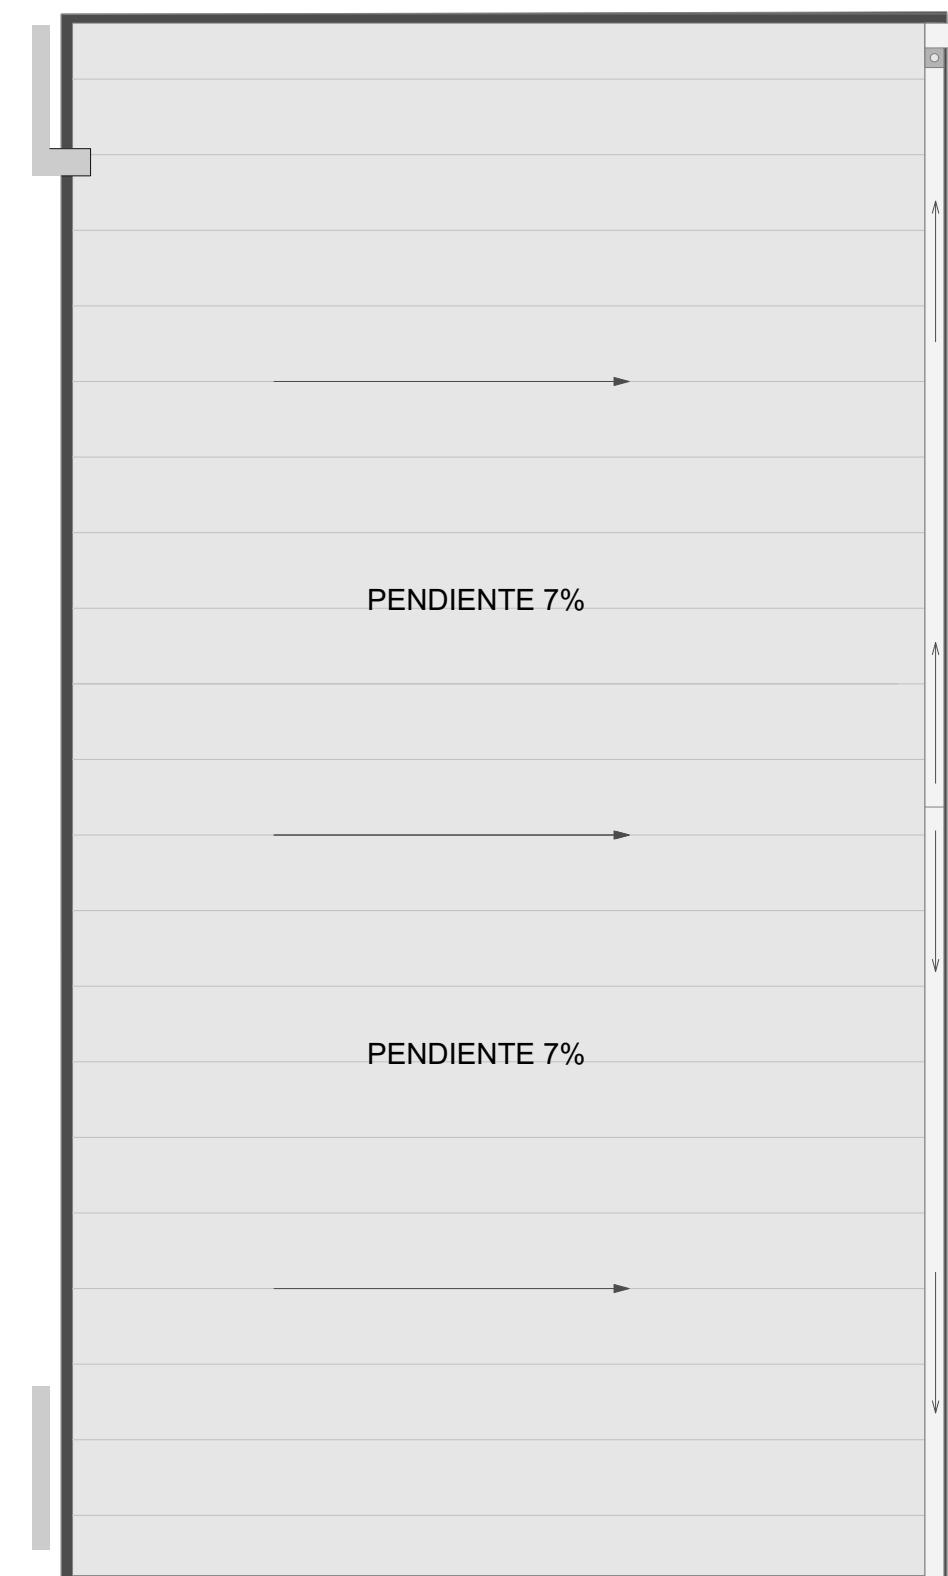

VISTA

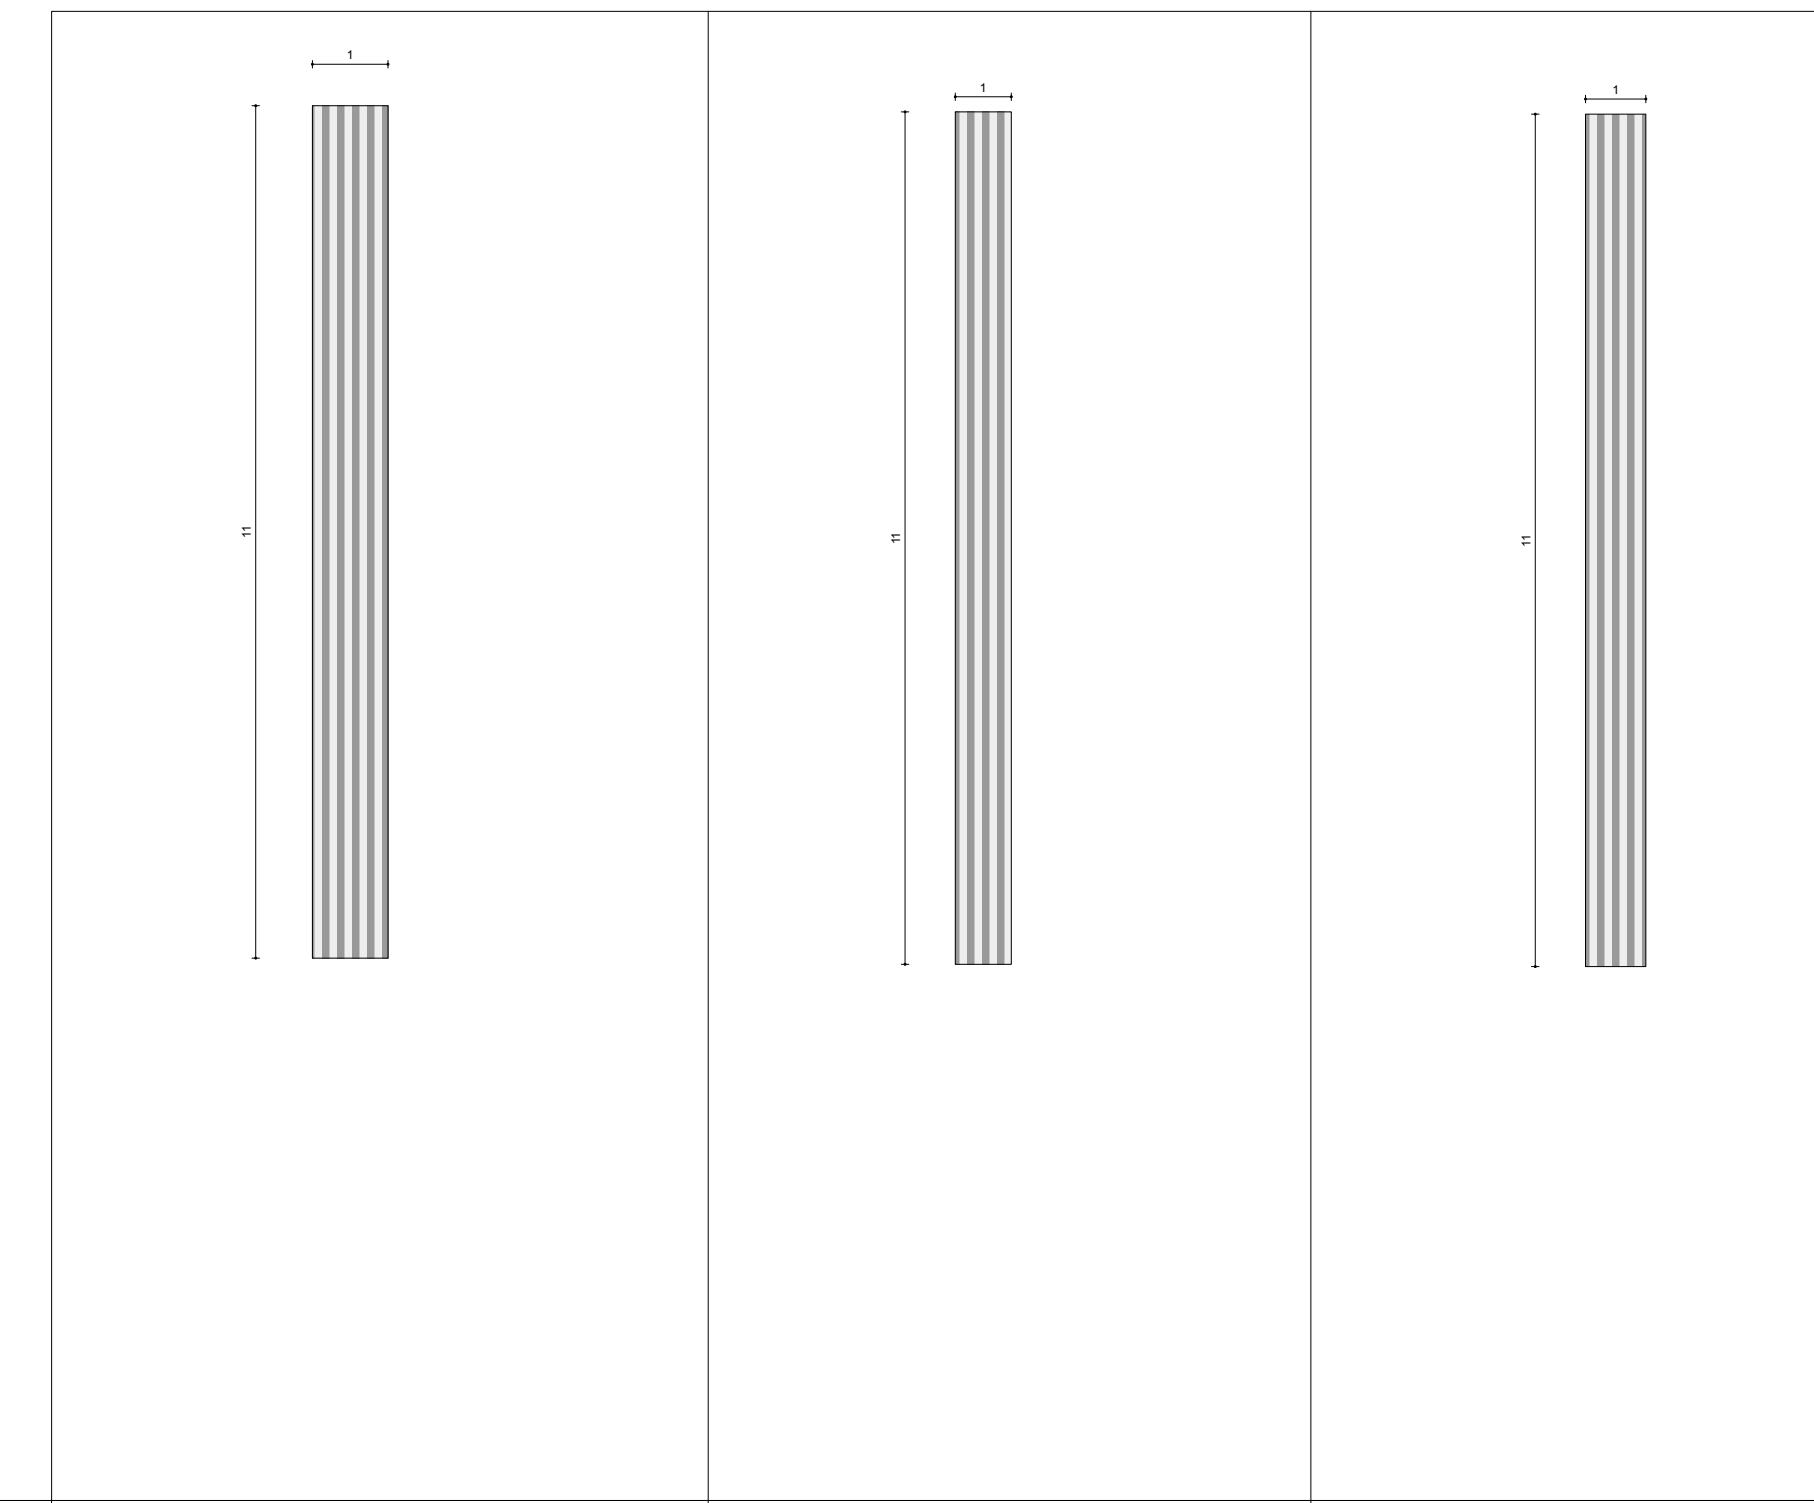

	<b>TIPO</b>	PANEL 1*11,277	PANEL 0,741 *11,277	PANEL 0,798 *11,277
	<b>CANTIDAD</b>	32 (treinta y dos)	1 (uno)	1 (uno)
	<b>COLOR</b>	Gris grafito	Gris grafito	Gris grafito

4


PLANTA DE TECHOS NORTE

Scale: 1:100

JAPAZ  
GUERRA  
ARQUITECTOS

OBRA:  
**ARIZU**


GODOY CRUZ / MENDOZA

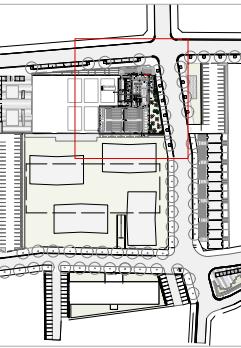

## PLANO:


EEQIA


ESCALA

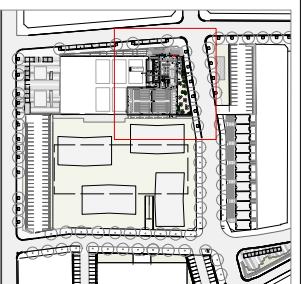

PLANO:  
DETALLE Y  
COMPUTO DE  
CARPINTERIAS  
DE ALUMINIO

FECHA	
ESCALA	1/125
PLANO N°	G.11
REV.	

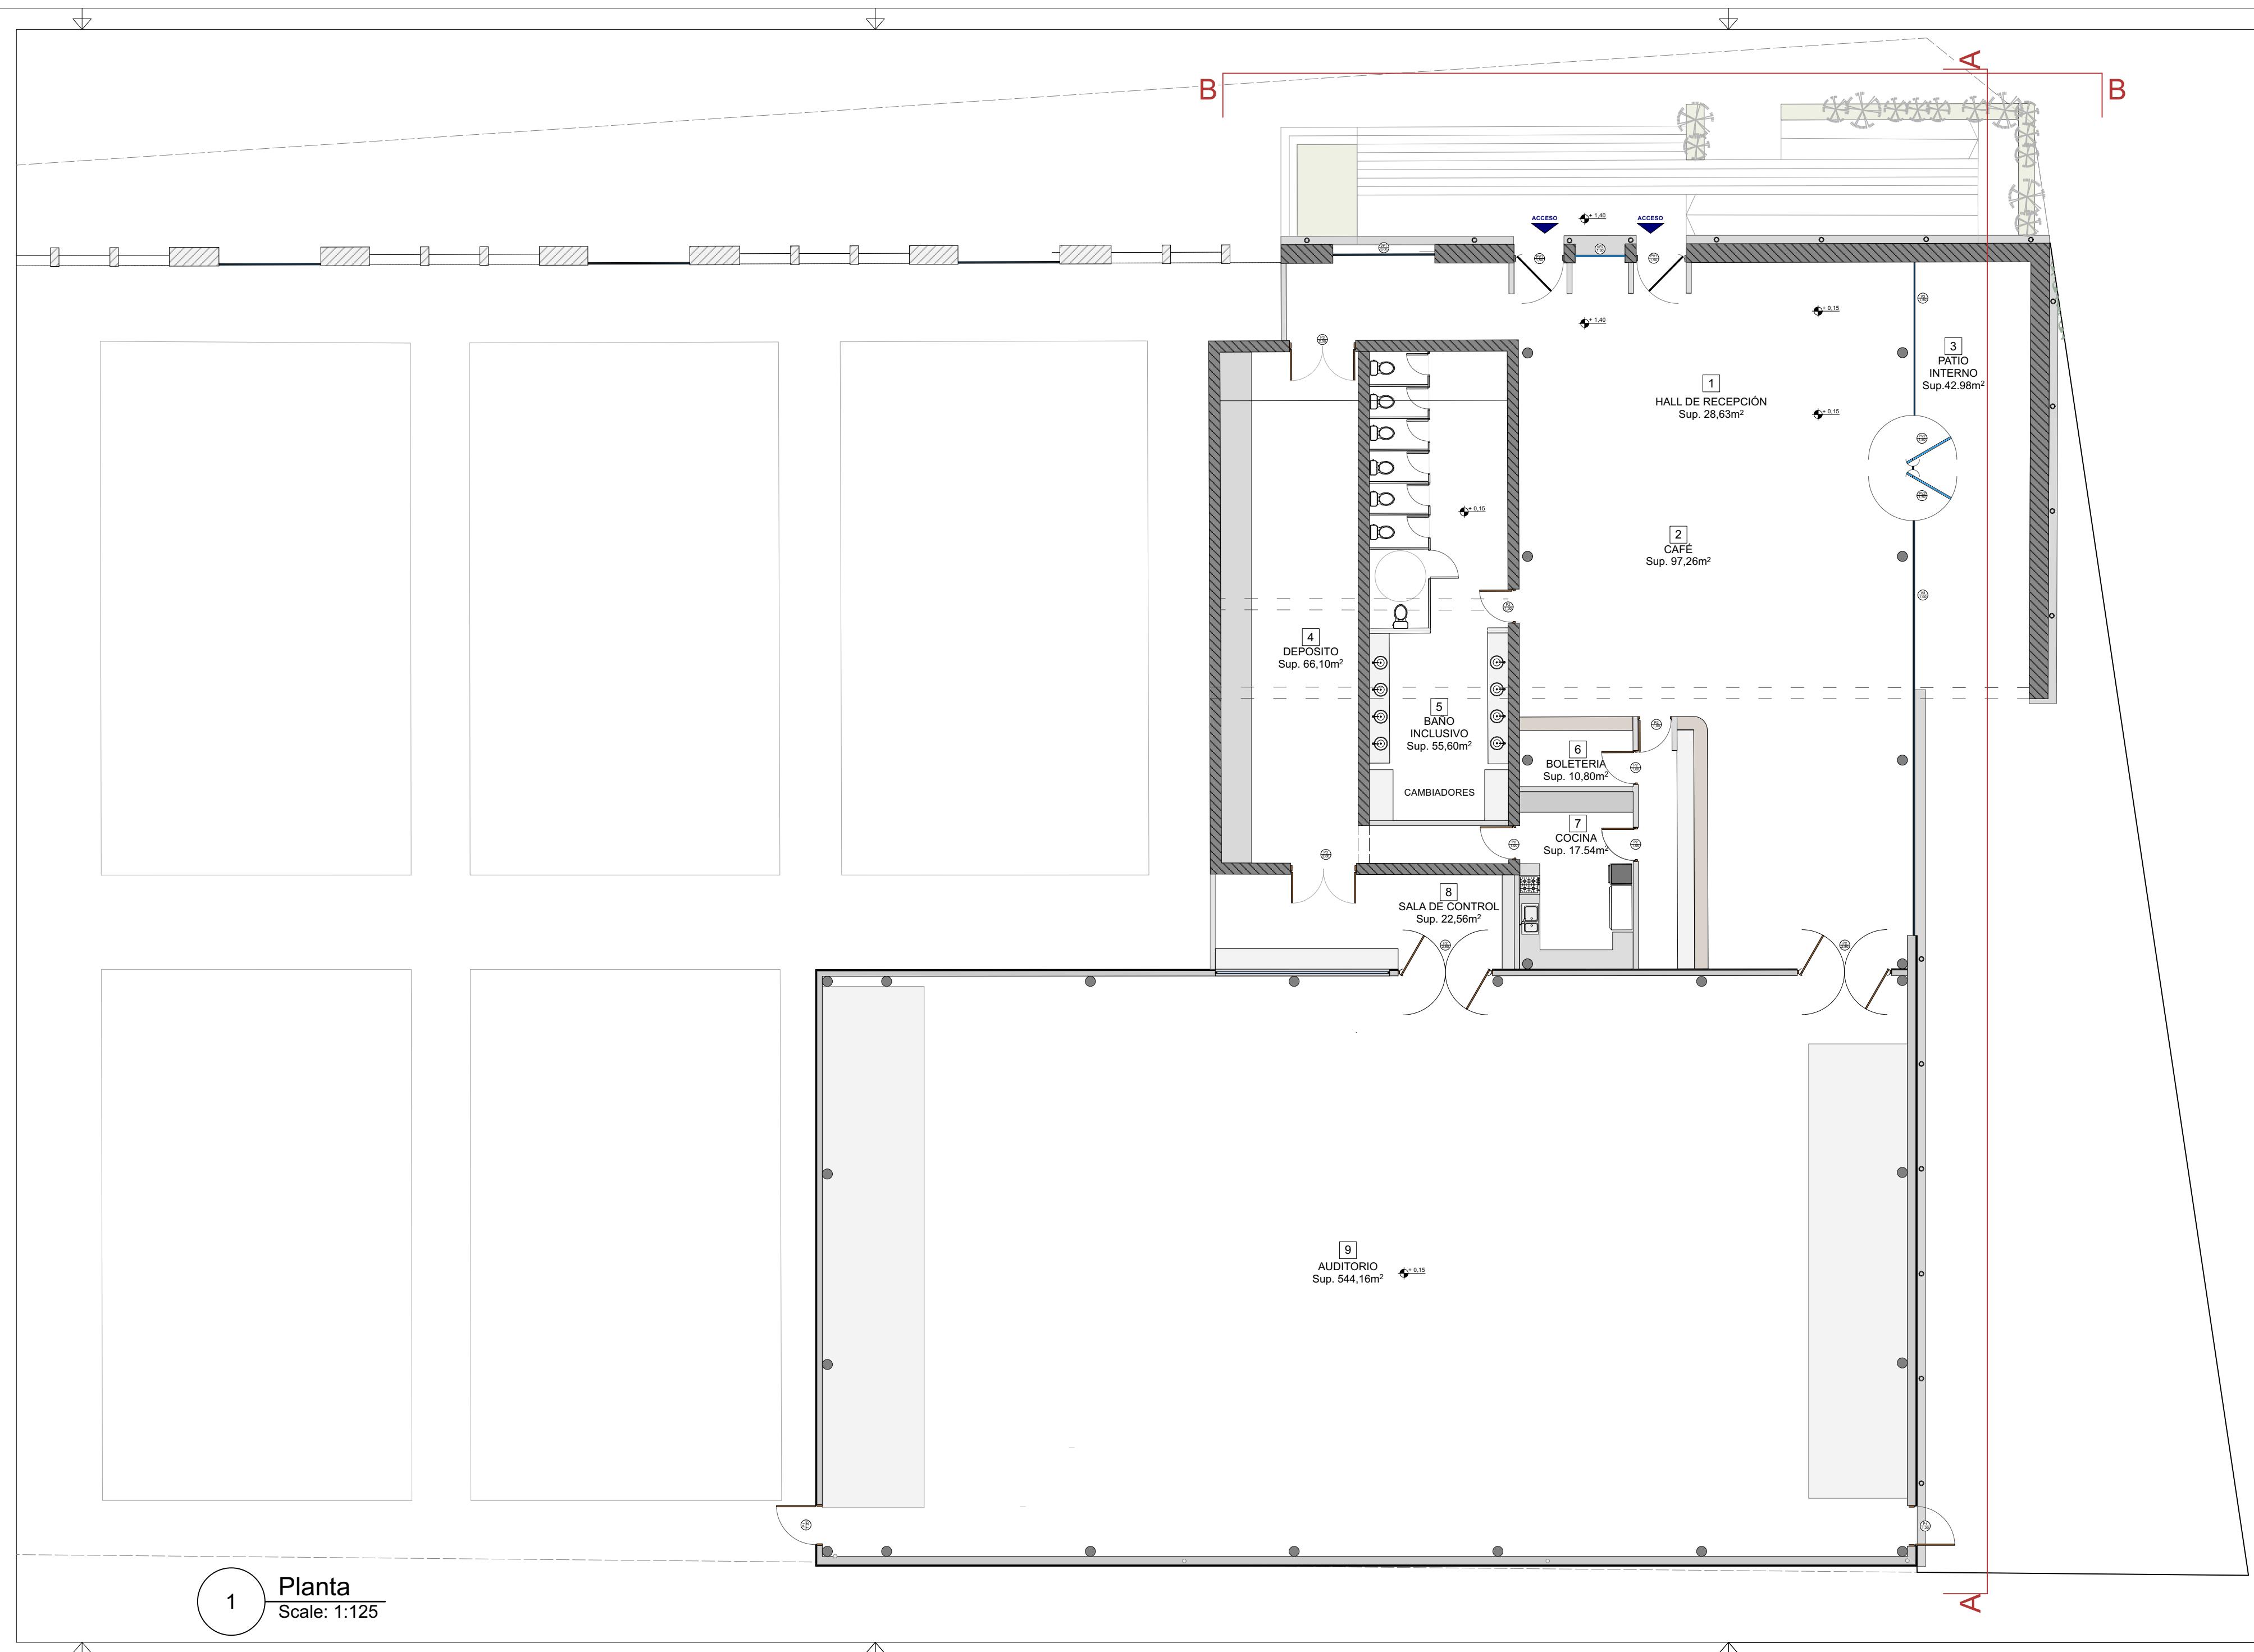

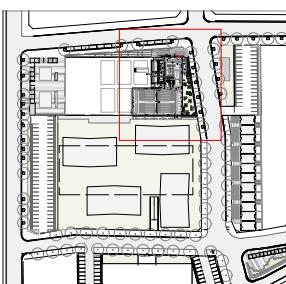

## CARPINTERÍAS - VISTA A-A

DESIGNACIÓN	V3 1,50	PF1 1,50	AJ 0,36	PV2 1,00
VISTA GENERAL				
VISTA				
TIPO	MURO CORTINA, PAÑO DE ABRIR	MURO CORTINA, PAÑO FIJO	MURO CORTINA, PAÑO FIJO	MURO CORTINA, PUERTAS DE REBATIR
CANTIDAD	18 (dieciocho)	44 (cuarenta y cuatro)	4 (cuatro)	1 (uno)
MODO DE ABRIR	Ventanas Proyectante con brazo de empuje	Paños Fijos	Paños Fijos	Puerta de rebatir
PERFIL	Alumino Anodizado Marca: Aluar - Modelo: Frame Color: Negro	Alumino Anodizado Marca: Aluar - Modelo: Frame Color: Negro	Alumino Anodizado Marca: Aluar - Modelo: Frame Color: Negro	Alumino Anodizado Marca: Aluar Modelo: New30 Color: Negro
VIDRIO	Exterior: Eclipse Advantange Gris 6mm Templado Camara de Aire: 12mm Interior: Laminado 5+5mm incoloro	Exterior: Eclipse Advantange Gris 6mm Templado Camara de Aire: 12mm Interior: Laminado 5+5mm incoloro	Exterior: Eclipse Advantange Gris 6mm Templado Camara de Aire: 12mm Interior: Laminado 5+5mm incoloro	Exterior: Eclipse Advantange Gris 6mm Templado Camara de Aire: 12mm Interior: Laminado 5+5mm incoloro
UBICACIÓN	Vista A-A	Vista A-A	Vista A-A	Vista A-A


2 VISTA A-A  
Scale: 1:100

PLANO:  
DETALLE Y  
COMPUTO DE  
CARPINTERIAS  
DE ALUMINIO

FECHA

ESCALA 1/100

PLANO N° G.12 REV.

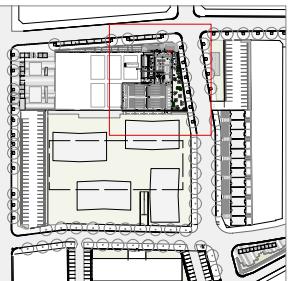

## CARPINTERÍAS - VISTA B-B

DESIGNACIÓN	V4 1,50	VF2 1,50	PV1 1,50	VF1 3,00
VISTA GENERAL				
VISTA				
TIPO	VENTANA DE ABRIR	VENTANA FIJA	PUERTA VENTANA	VENTANA FIJA
CANTIDAD	4 (cuatro)	1 (uno)	1 (uno)	1 (uno)
MODO DE ABRIR	Ventanas Proyectante con brazo de empuje	Paños Fijos	Puerta de rebatir	Ventana fija
PERFIL	Aluminio Anodizado Marca: Aluar - Modelo: Frame Color: Negro	Aluminio Anodizado Marca: Aluar - Modelo: Frame Color: Negro	Aluminio Anodizado Marca: Aluar Modelo: New30 Color: Negro	Aluminio Anodizado Marca: Aluar Modelo: New30 Color: Negro
VIDRIO	Exterior: Eclipse Advantange Gris 6mm Templado Camara de Aire: 12mm Interior: Laminado 4+4mm incoloro	Exterior: Eclipse Advantange Gris 6mm Templado Camara de Aire: 12mm Interior: Laminado 4+4mm incoloro	Exterior: Eclipse Advantange Gris 6mm Templado Camara de Aire: 12mm Interior: Laminado 4+4mm incoloro	Exterior: Eclipse Advantange Gris 6mm Templado Camara de Aire: 12mm Interior: Laminado 4+4mm incoloro
UBICACIÓN	Vista A-A	Vista A-A	Vista A-A	Vista A-A


3 VISTA B-B  
Scale: 1:100

PLANO:  
DETALLE Y  
COMPUTO DE  
CARPINTERIAS  
DE ALUMINIO

FECHA


ESCALA 1/100

PLANO N° G.13 REV.

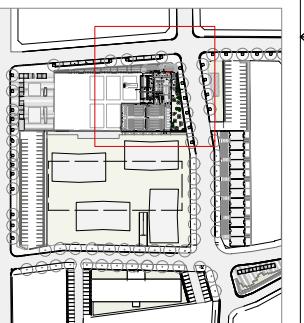

PLANO:  
Planta, detalle piso

FECHA  
ESCALA 1:125  
PLANO N° G.14 REV.

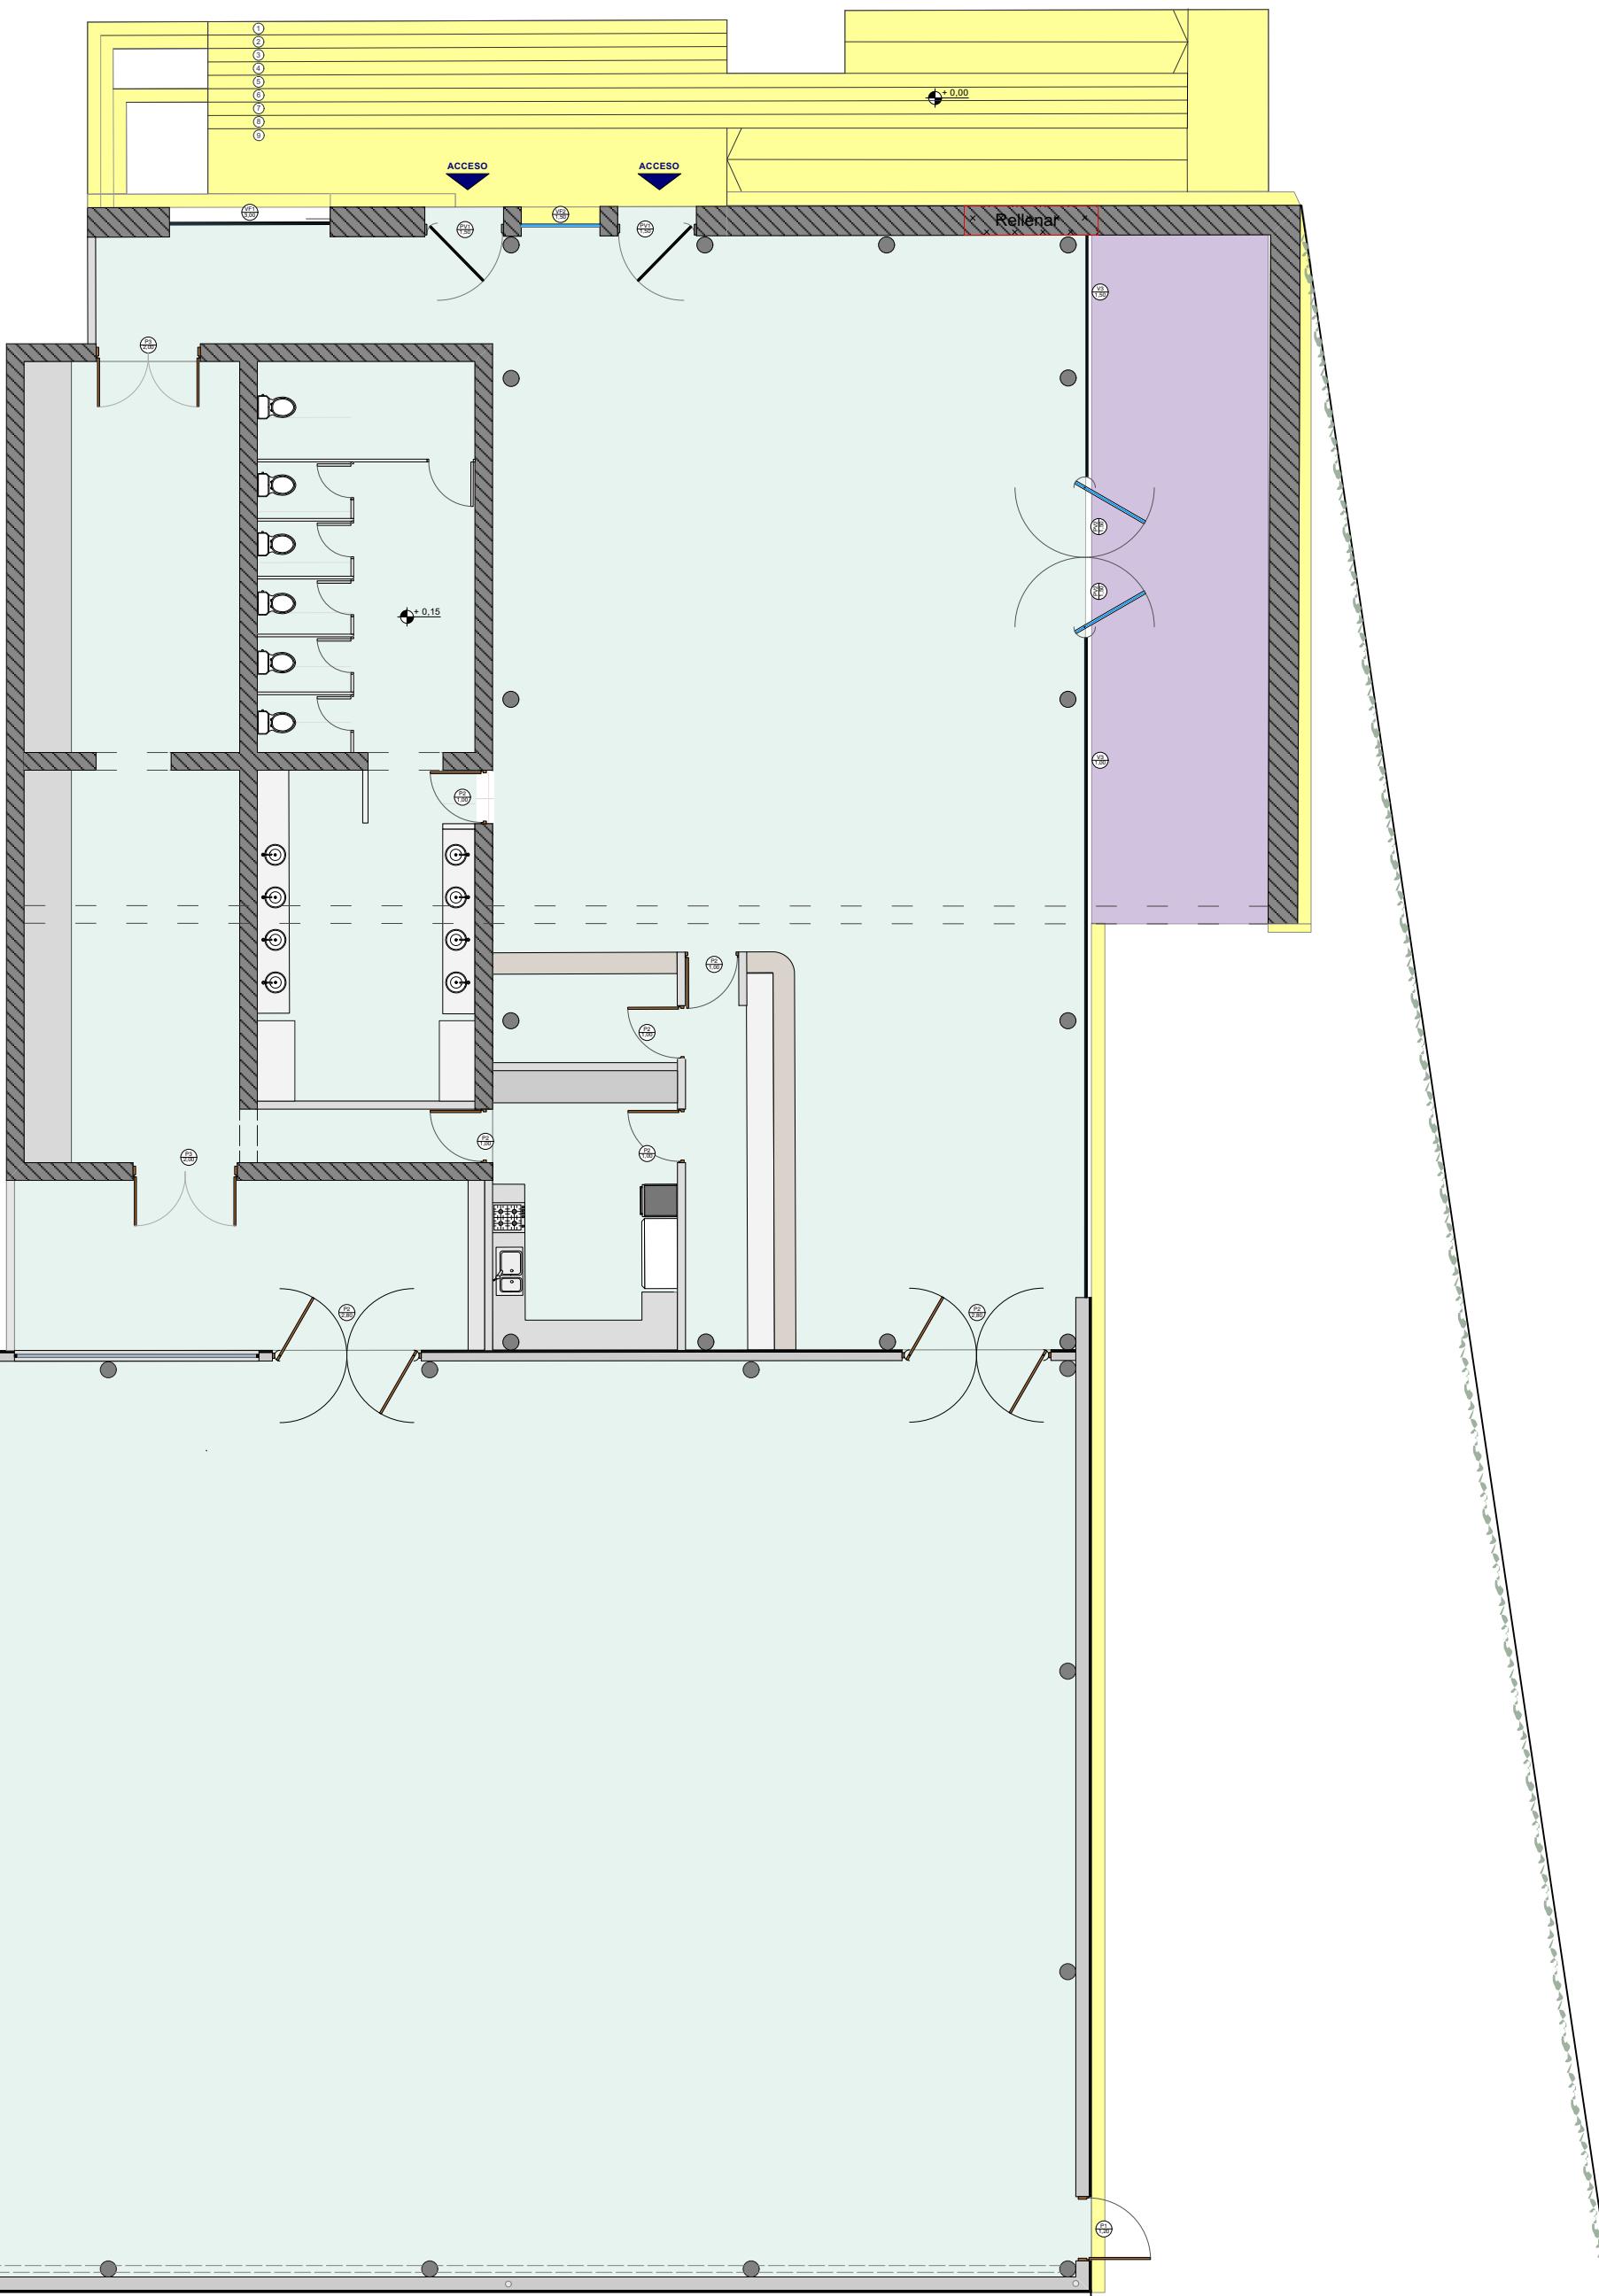

REF	MARCA	ARTEFACTO	IMAGEN	UNIDADES
	CERRO NEGRO	LONDON GRIS 117 X 58		960m <sup>2</sup> X 96m <sup>2</sup> (10% desperdicio) = 1037m <sup>2</sup>
	PORFIDO	BALDOSA PORFIDO 30 X 60		42,4m <sup>2</sup> X 4,2m <sup>2</sup> (10% desperdicio) = 46,6m <sup>2</sup>
	CEMENTO PEINADO			67,5m <sup>2</sup>

1 Planta, detalle pisos  
Scale: 1:125

# PROLONGACIÓN DE CALLE AGUSTÍN ALVAREZ

JAPAZ  
GUERRA  
ARQUITECTOS

## OBRA:

# ARIZU

GODOY CRUZ / MENDOZA




**PLANO:**



**FECHA**

ESCALA 1/125


PLANO N° G.15

Digitized by srujanika@gmail.com

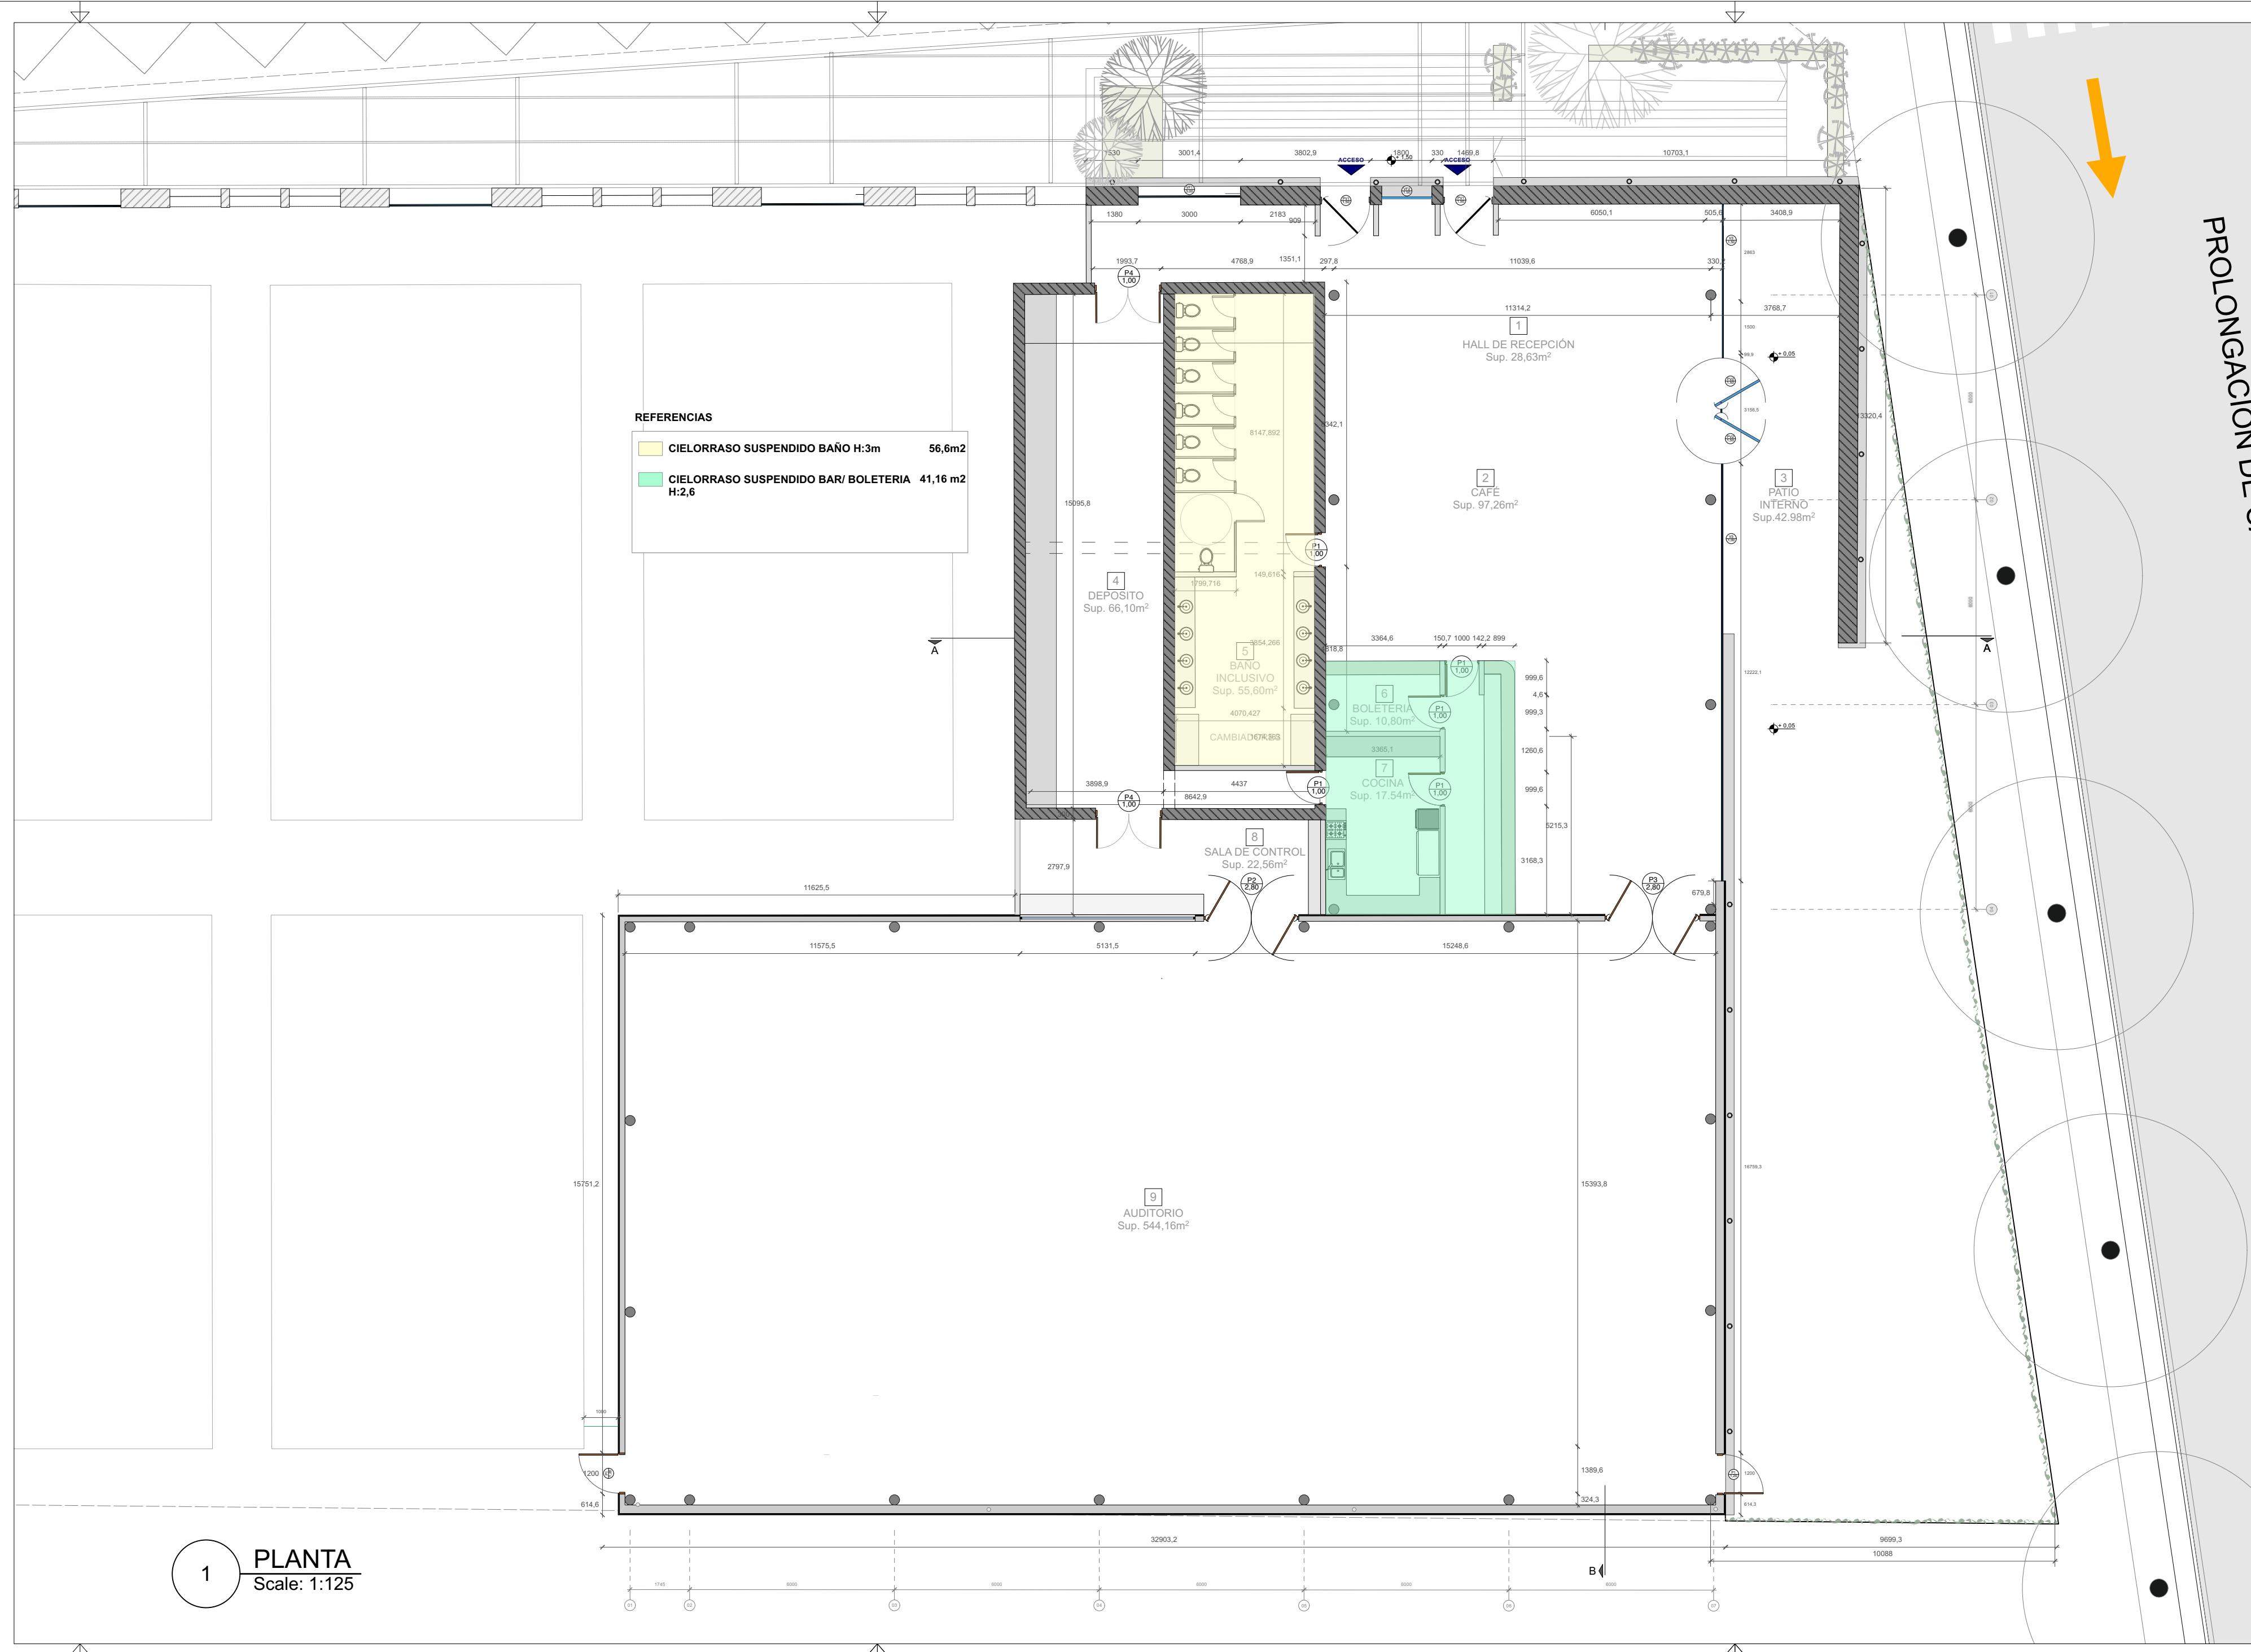


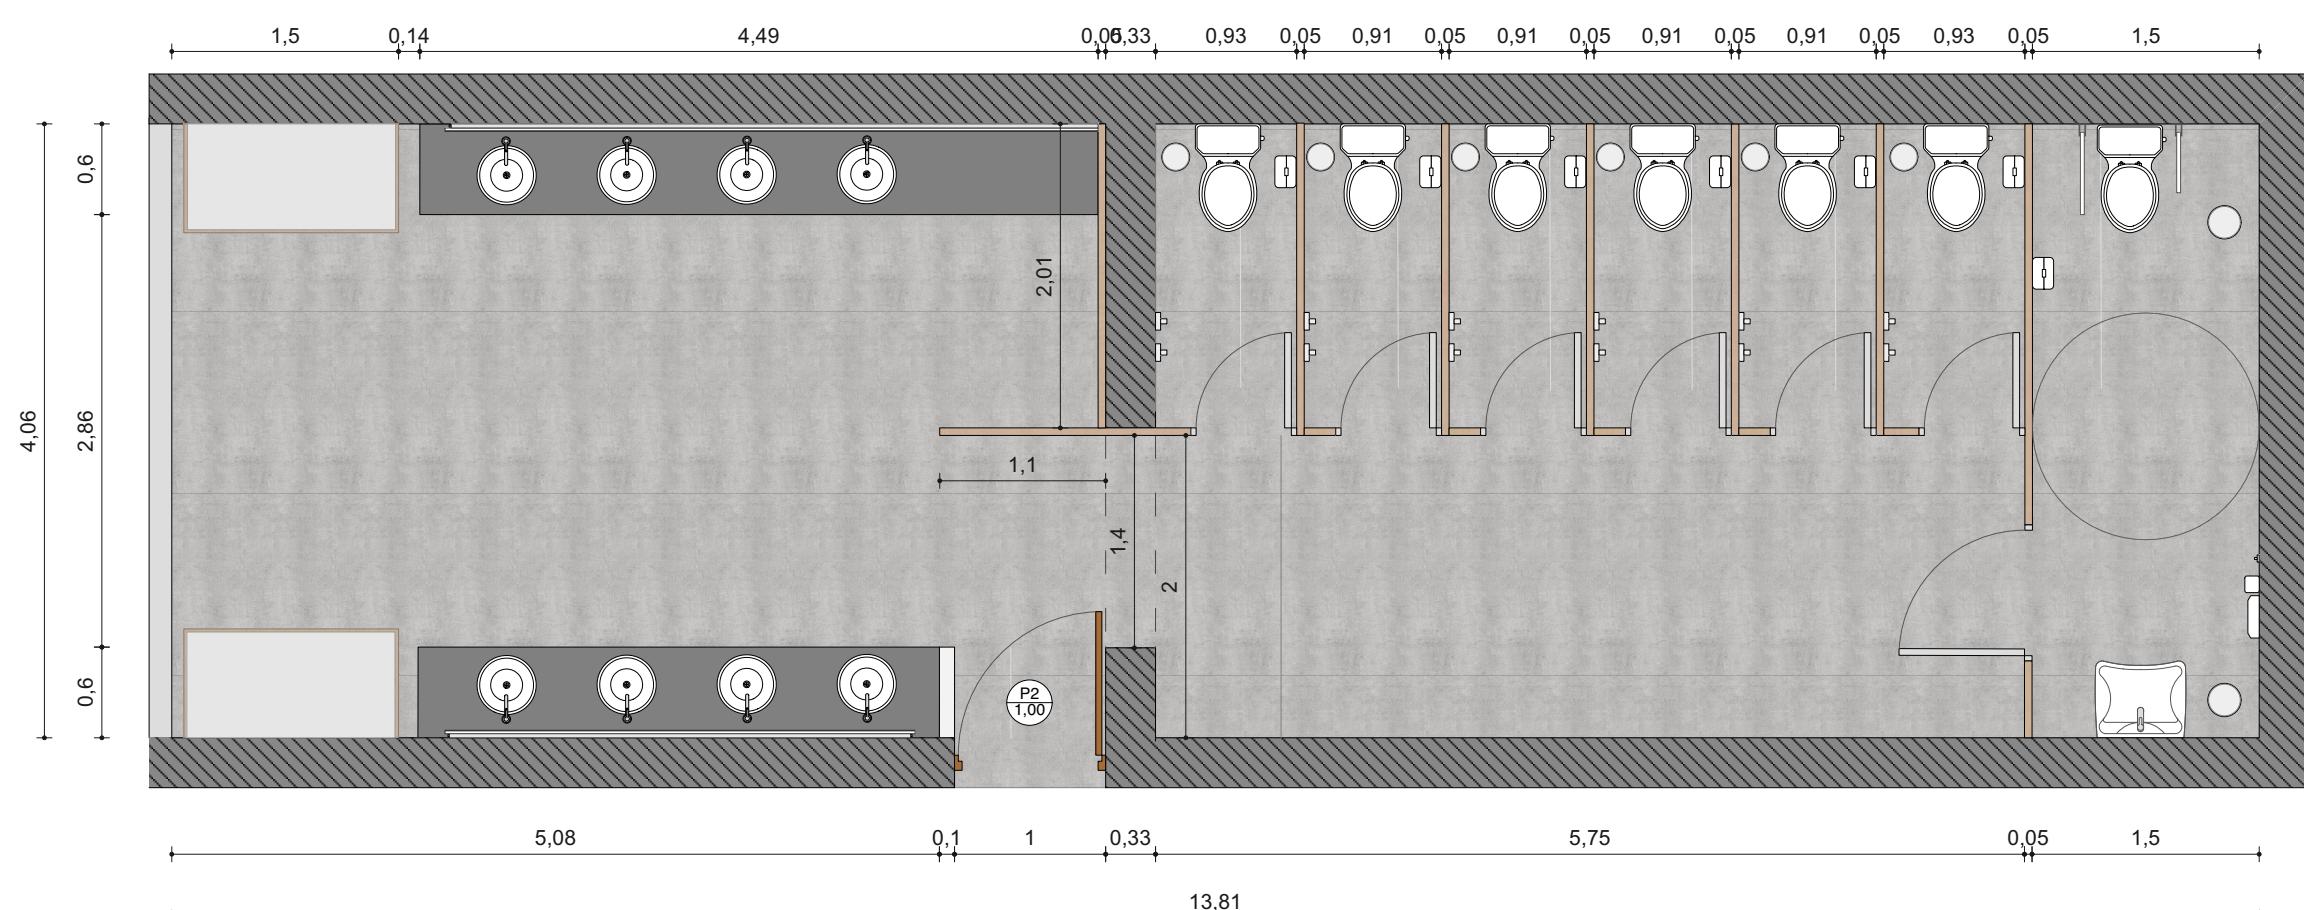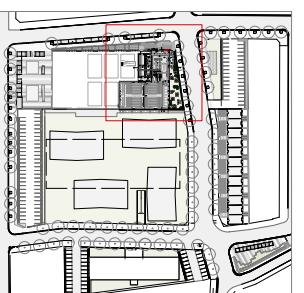

1 Planta sanitario  
Scale: 1:50

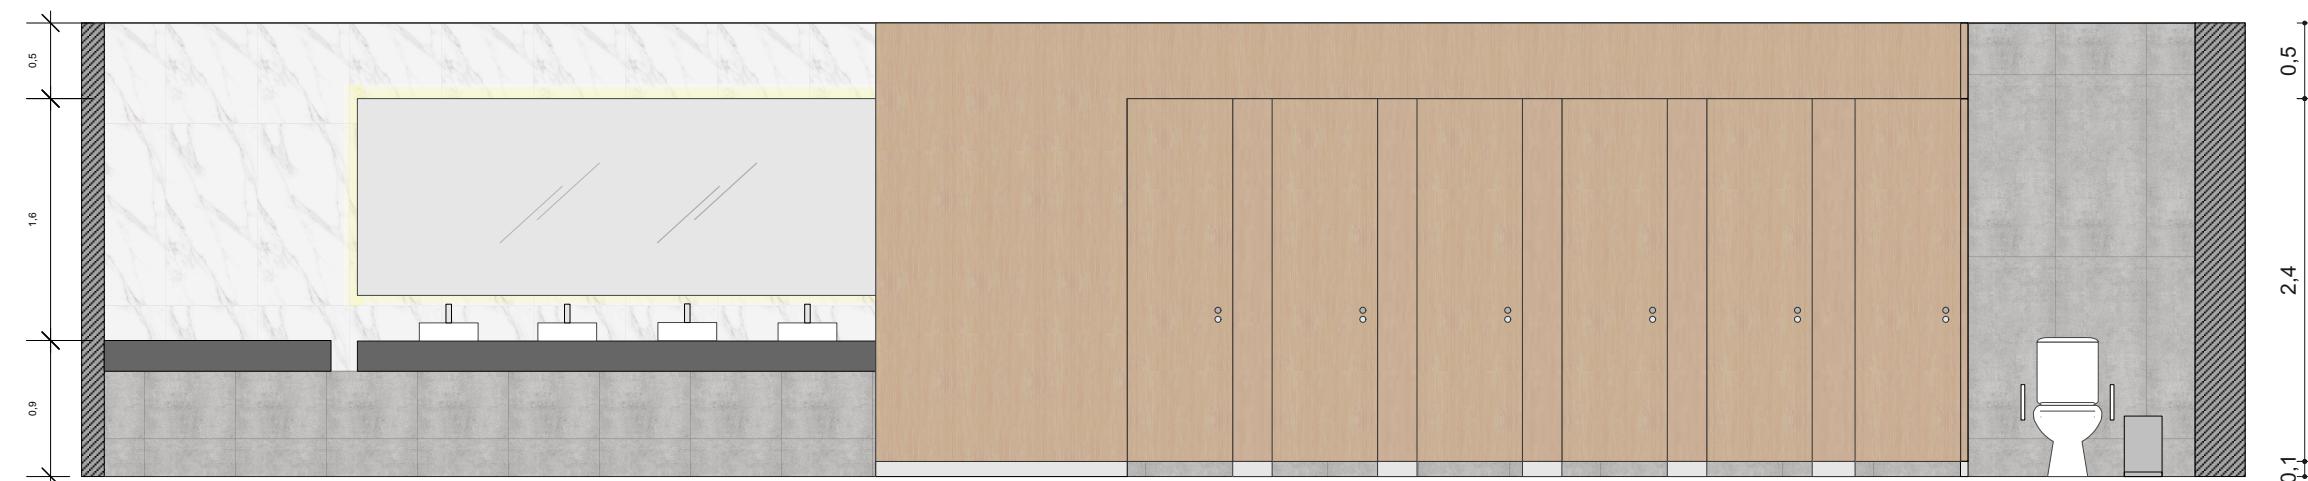

2 Vista 1  
Scale: 1:50

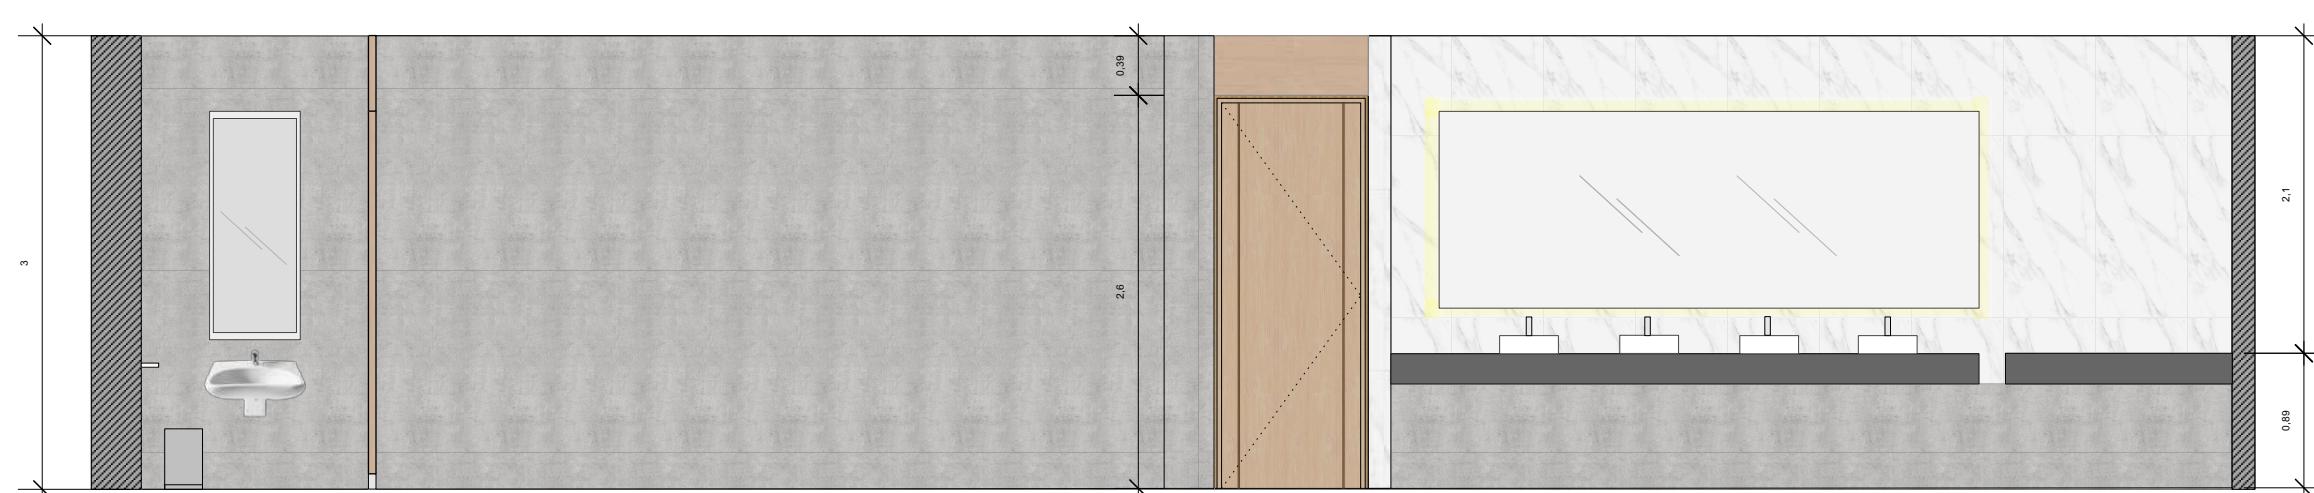

3 Vista 2  
Scale: 1:50

#### REFERENCIAS SANITARIO

Inodoro largo dama senso. Roca  
Bacha de apoyar Tori redonda 365mm Ferrum  
Griferia FV Tronic electronico  
Mesada en Granito Negro Brasil leather de 2,3m2  
Tachos de basura acero inoxidable  
Dispenser de papel higienico  
Dispenser de jabon  
Dispenser de papel  
Secador de manos  
Espejo con iluminacion led 3,60 x1,30

cant. 6  
cant. 8  
cant. 8  
cant. 2  
cant. 9  
cant. 6  
cant. 2  
cant. 1  
cant. 1  
cant. 2

#### BAÑO MOVILIDAD REDUCIDA

Inodoro Access Roca  
Lavatorio Access Roca  
Griferia FV Tronic electronico  
Tacho de basura acero inoxidable  
Percha FV Cafayate  
Dispenser de papel higienico  
Dispenser de jabon  
Dispenser de papel  
Espejo basculante 0,60x0,80  
Kit seguridad baño (barrales)


cant. 1  
cant. 1

#### PORCELLANATO PAREDES


CERRO NEGRO, London gris 58 117 68,77 (10%) = 75,65m<sup>2</sup>  
CERRO NEGRO, Partenón pulido 58 117 37,82 (10%) = 41,60m<sup>2</sup>

PLANO:  
Detalle sanitario

FECHA	
ESCALA	1/50
PLANO N°	G.16
REV.	

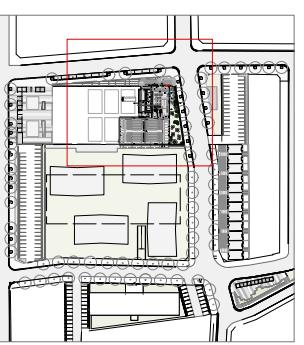

PROLONACIÓN DE CALLE AGUSTÍN ALVAREZ

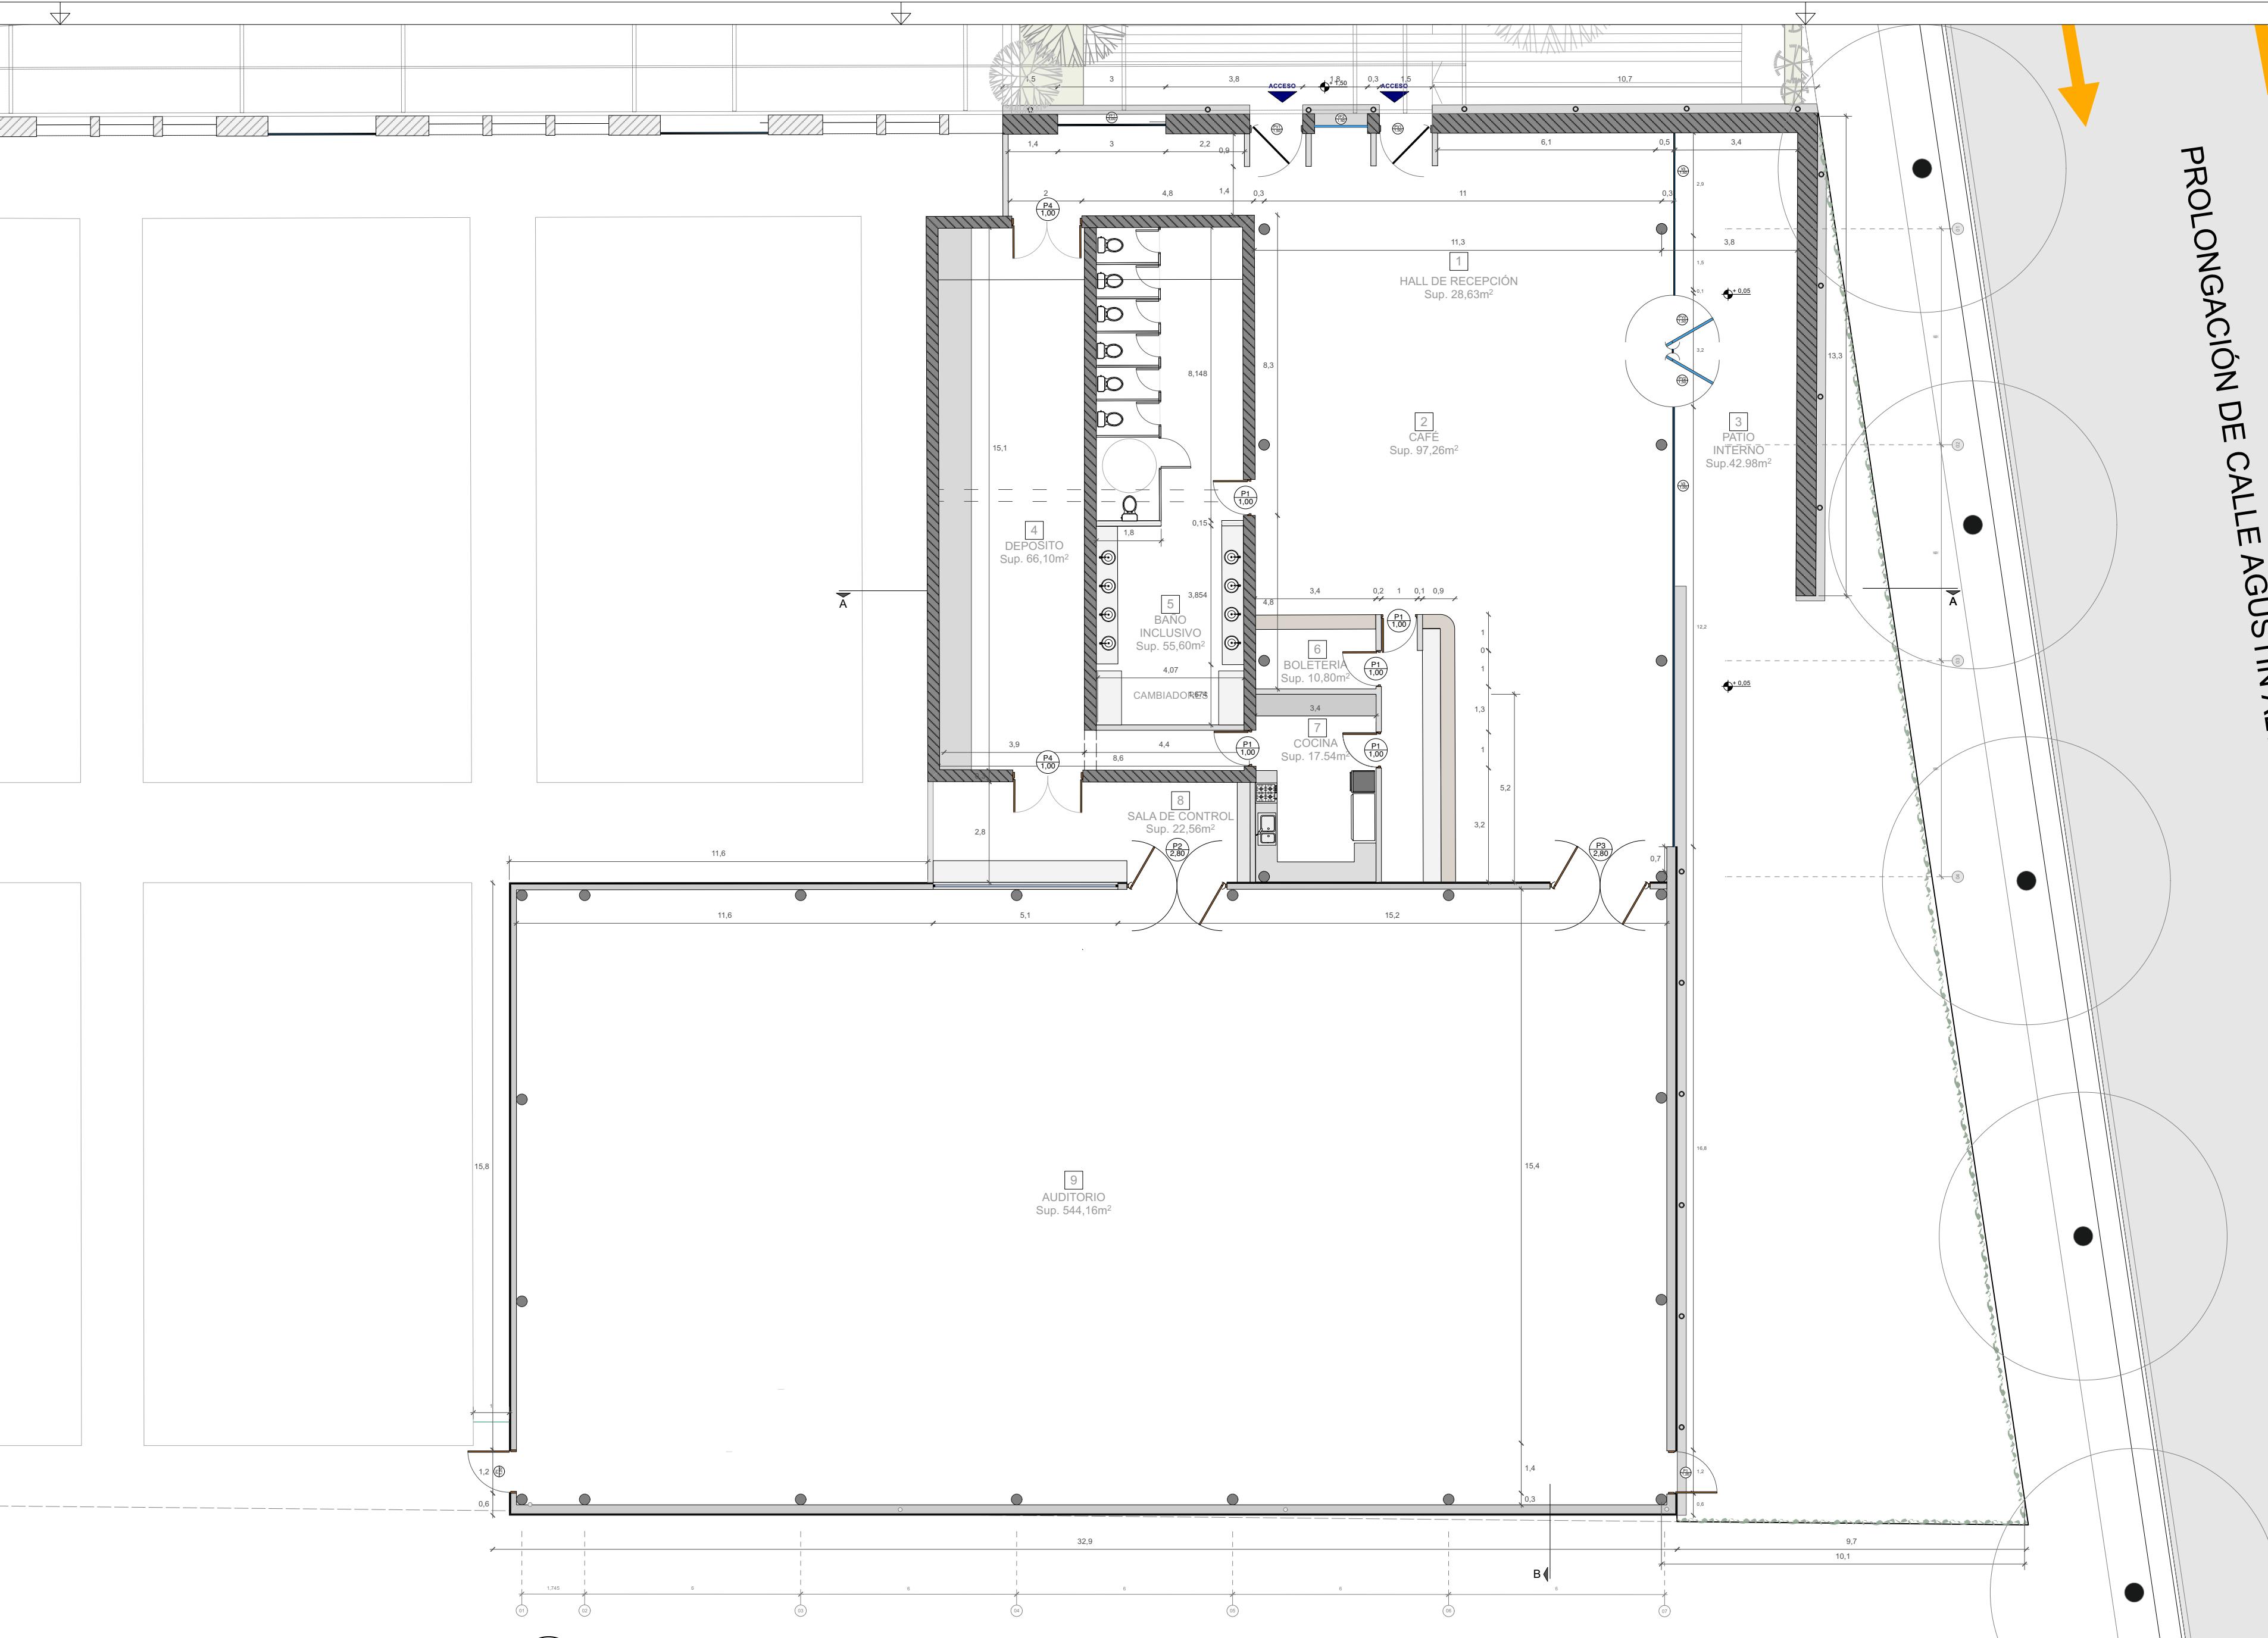


PLANO:  
Detalle puertas interiores


FECHA

ESCALA 1/125

PLANO N° G.17 REV.

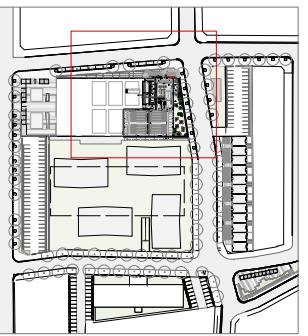


P 1

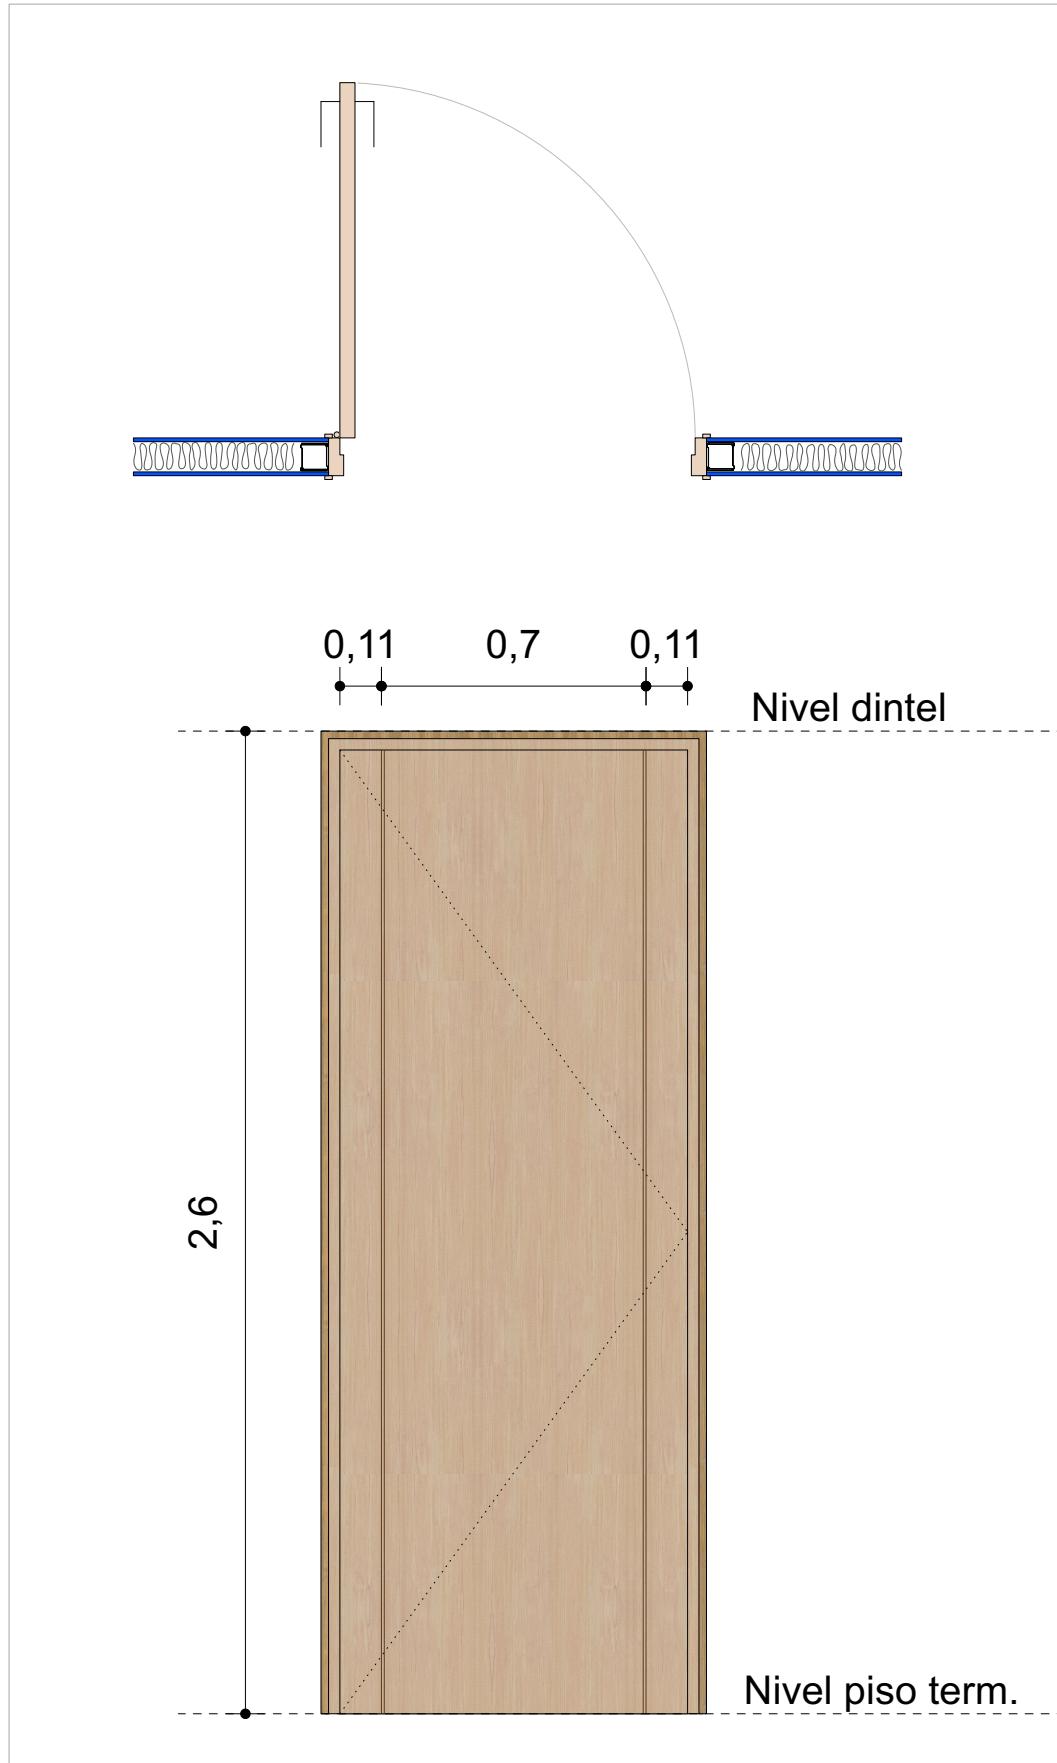

**PUERTA 1,00**  
Marco macizo de Laurel,  
puerta enchapada en Goiabao relleno nido  
de abeja o celulonico, borde macizo en peterib

ITEM	Planta Baja	TOTAL	Observaciones
Puerta 2.80	1	1	1 puerta doble vaiven

P 4

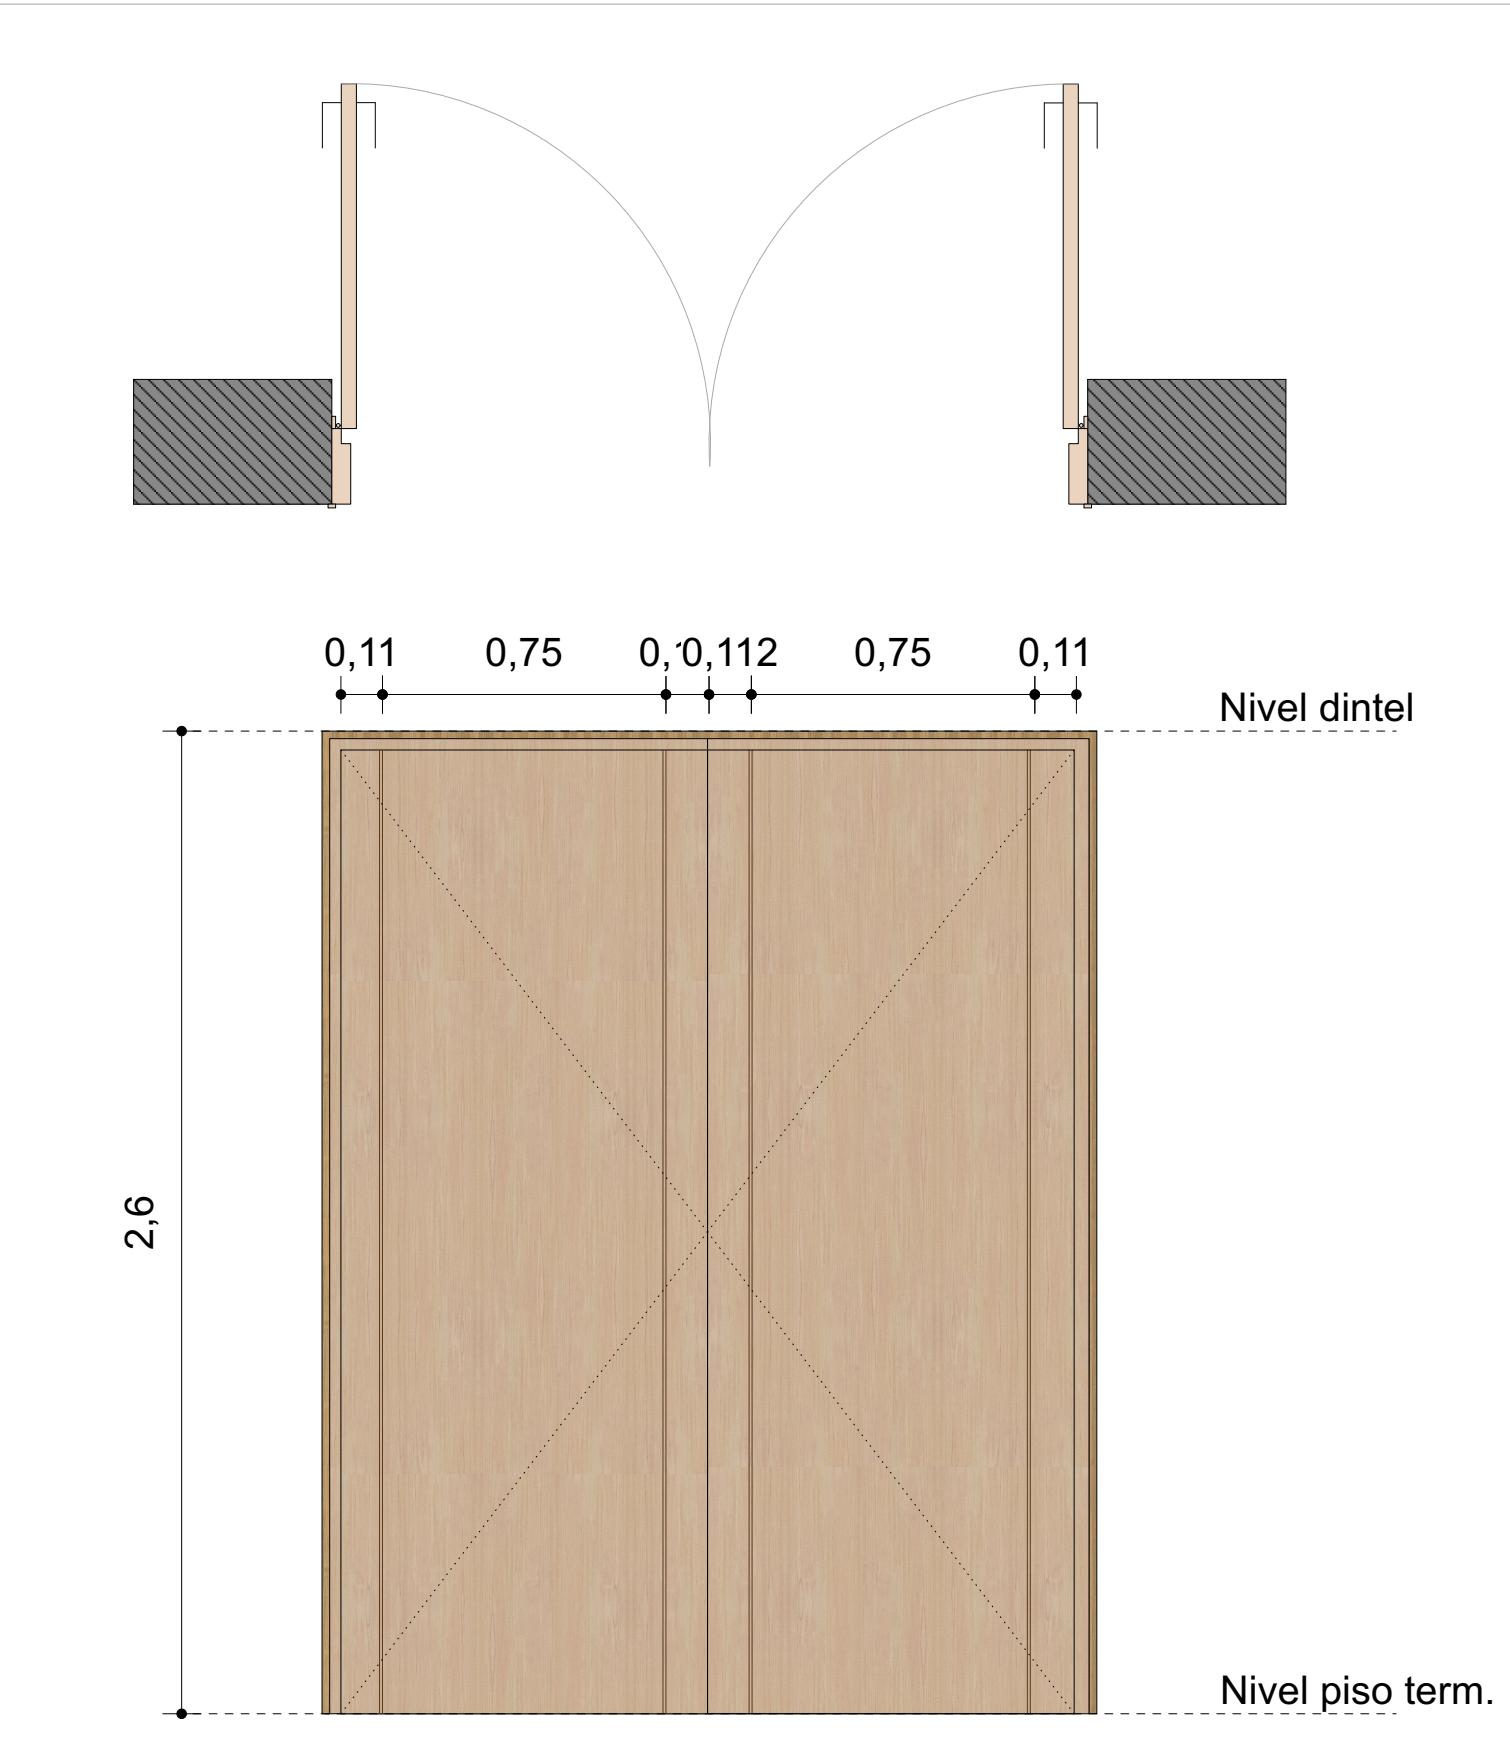

**PUERTA 2,00**  
Marco macizo de Laurel,  
puerta enchapada en Goiabao relleno nido  
de abeja o celulonico, borde macizo en peteribi


ITEM	Planta Baja	TOTAL	Observaciones
Puerta 2,80	1	1	1 puerta doble vaiven

#### **Detalle puertas interiores**


**FECHA**

ESCALA

PLANO N° G.18

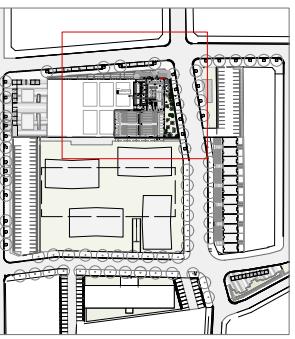


P 2

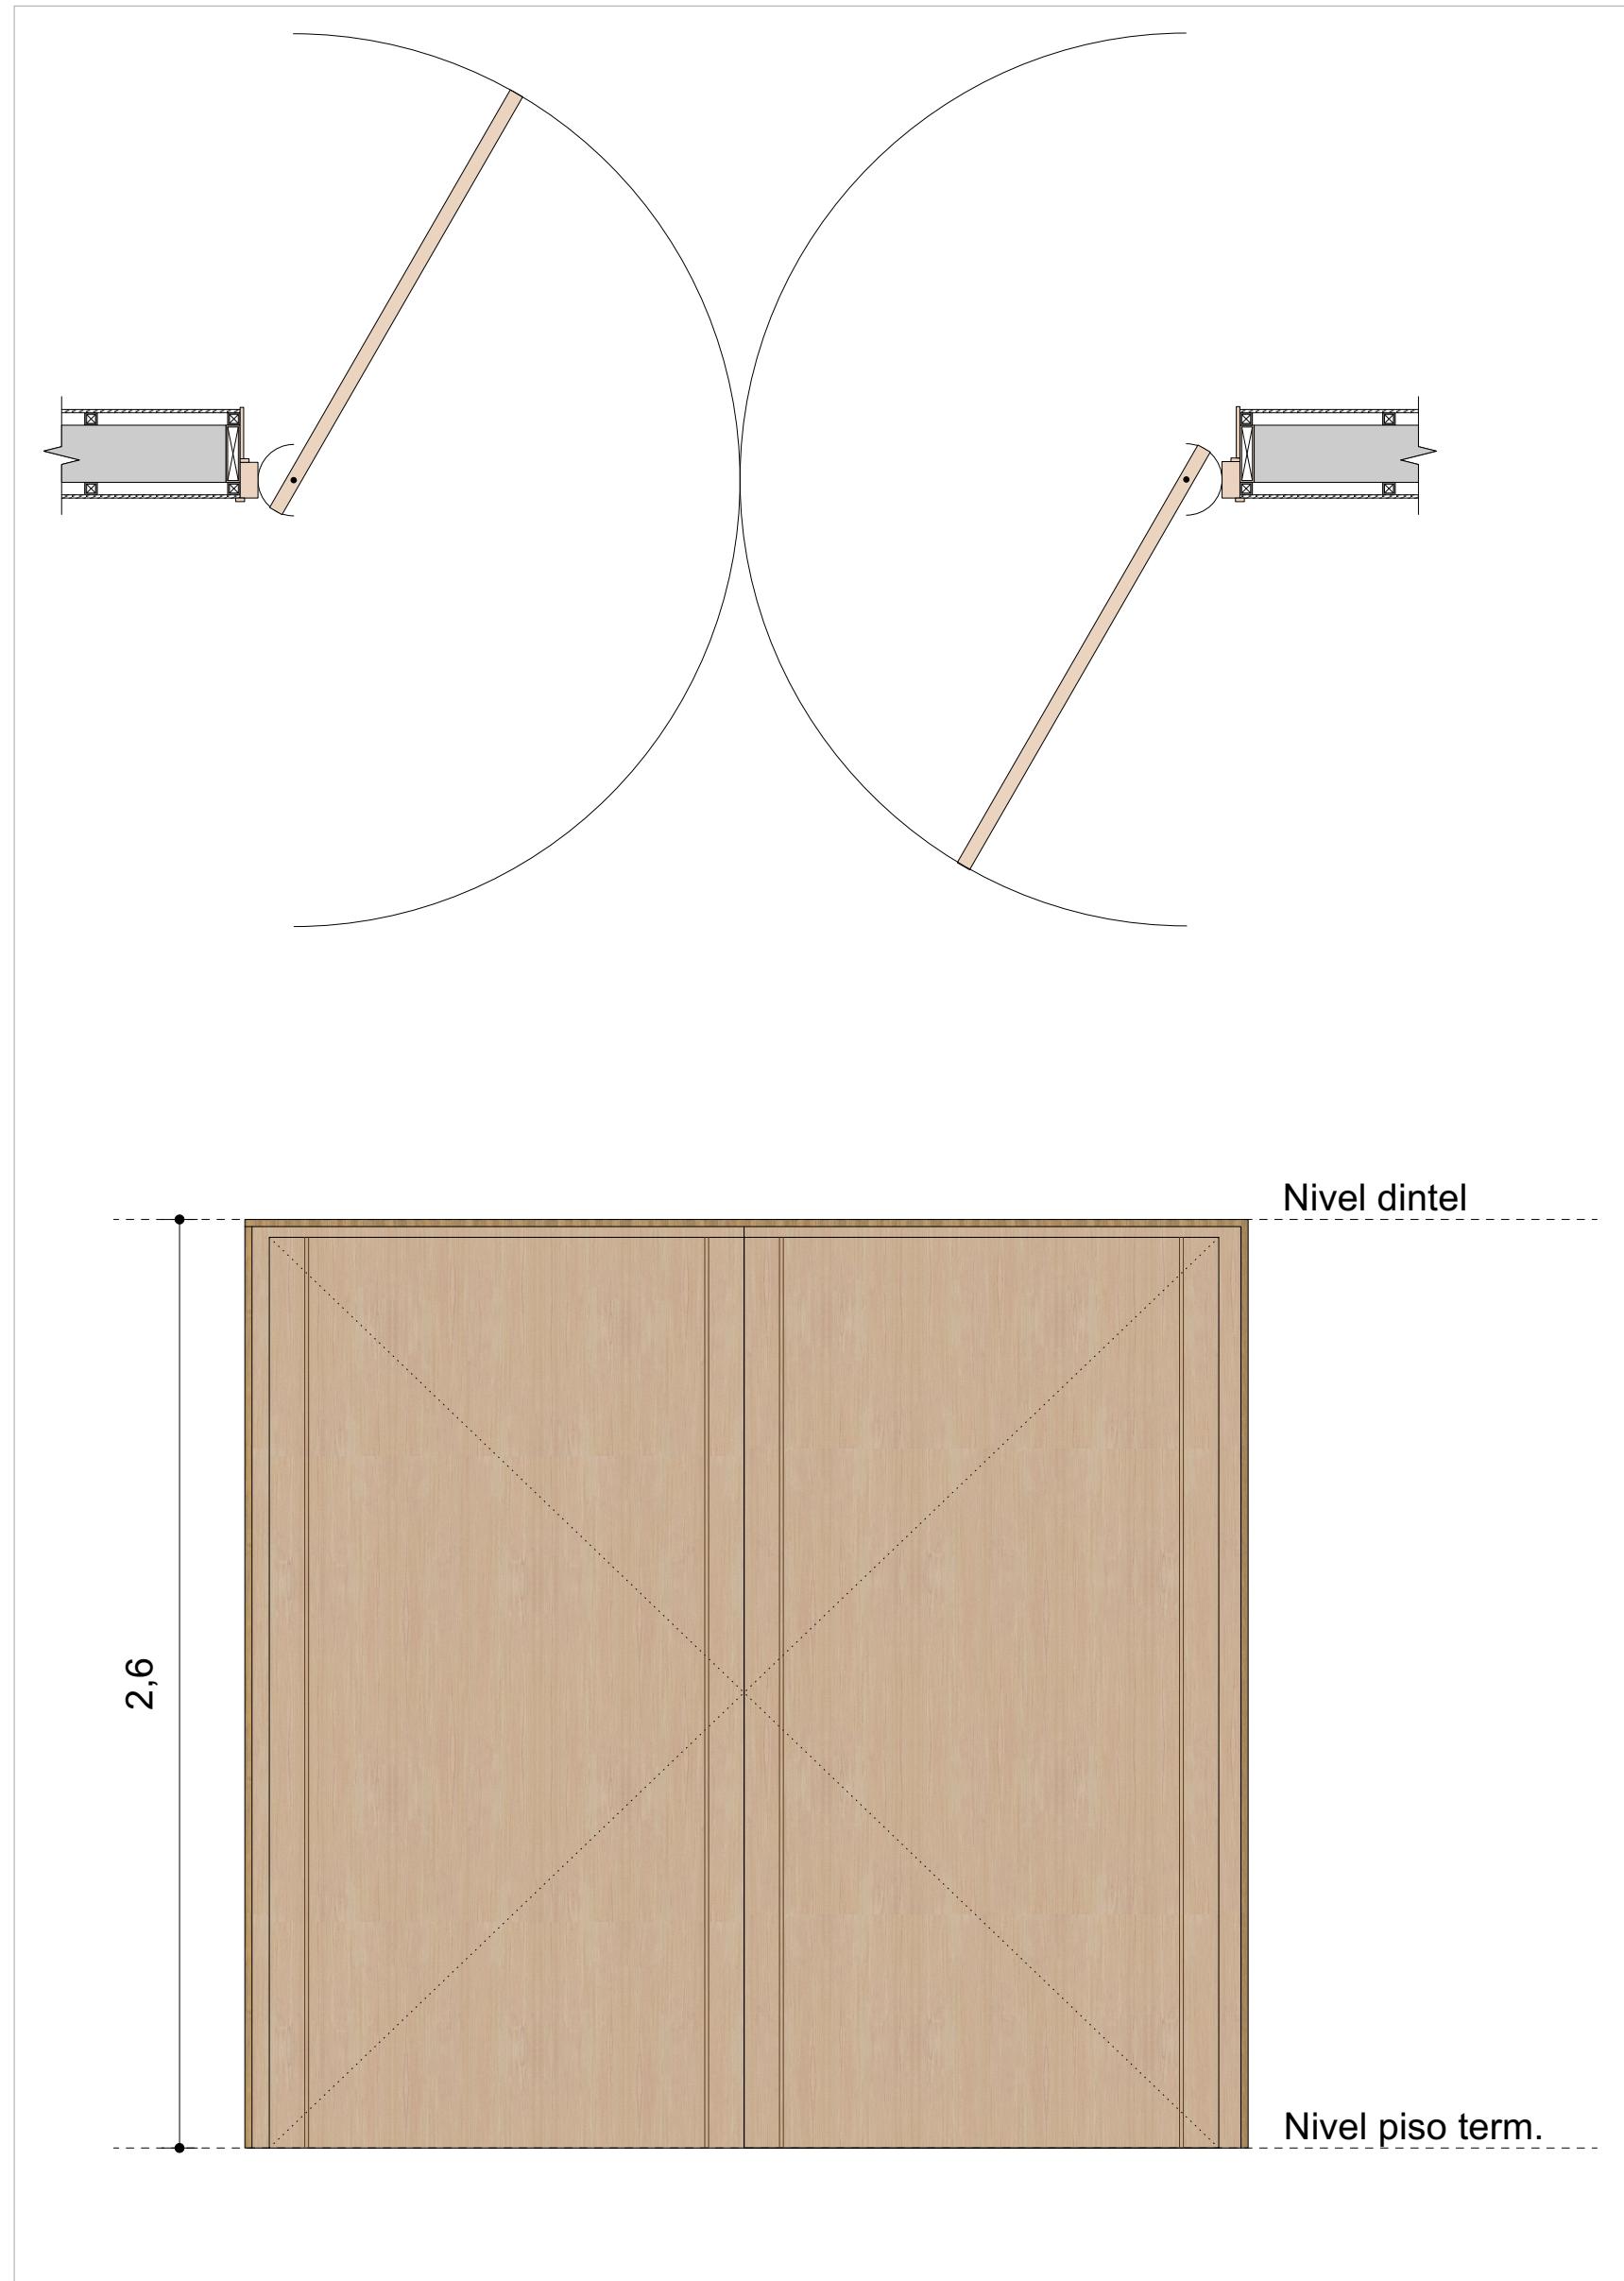

PUERTA 2,80  
Marco macizo de Laurel,  
puerta enchapada en Goiabao relleno nido  
de abeja o celulonico, borde macizo en peteribi


ITEM	Planta Baja	TOTAL	Observaciones
Puerta 2,80	1	1	1 puerta doble vaiven

P 3

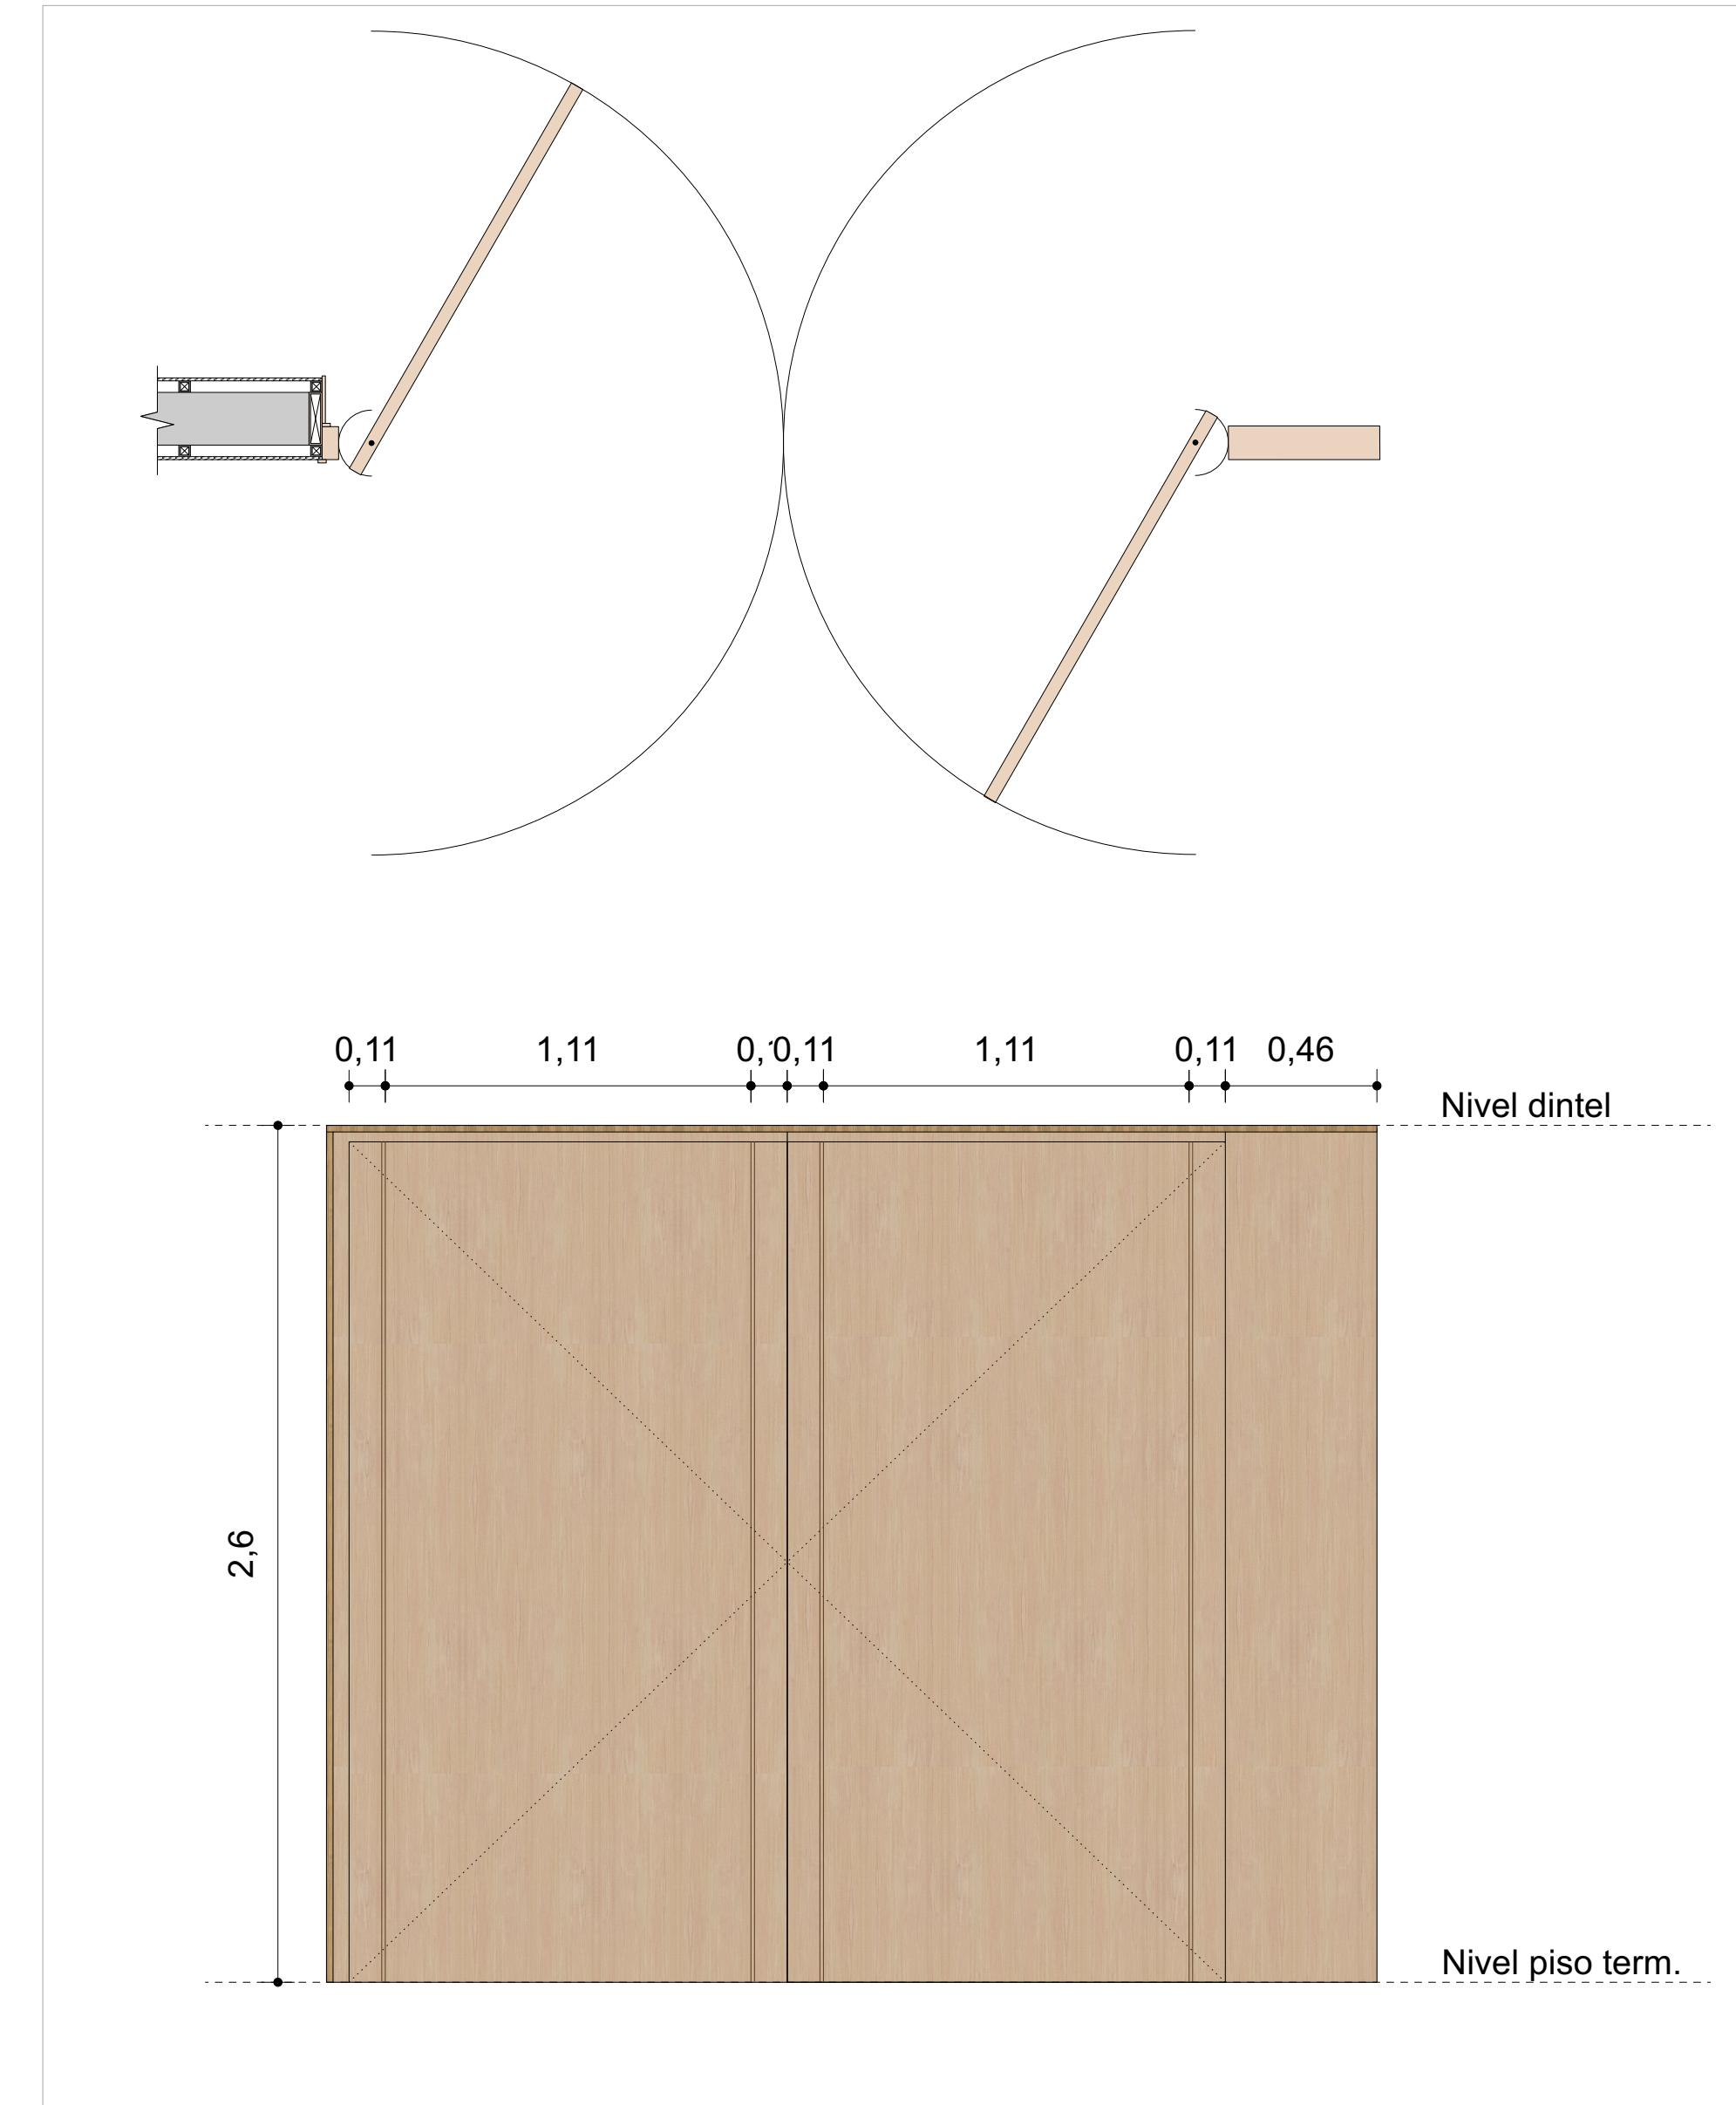

PUERTA 2,80 + PAÑO FIJO  
Marco macizo de Laurel,  
puerta enchapada en Goiabao relleno nido  
de abeja o celulonico, borde macizo en peteribi

ITEM	Planta Baja	TOTAL	Observaciones
Puerta 2,80	1	1	1 puerta doble vaiven

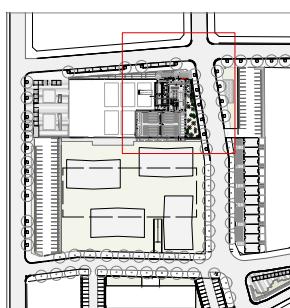

**PLANO:**

Detalle rampa de acceso

FECHA \_\_\_\_\_  
ESCALA 1:25  
PLANO N° G.20 | REV. \_\_\_\_\_

